

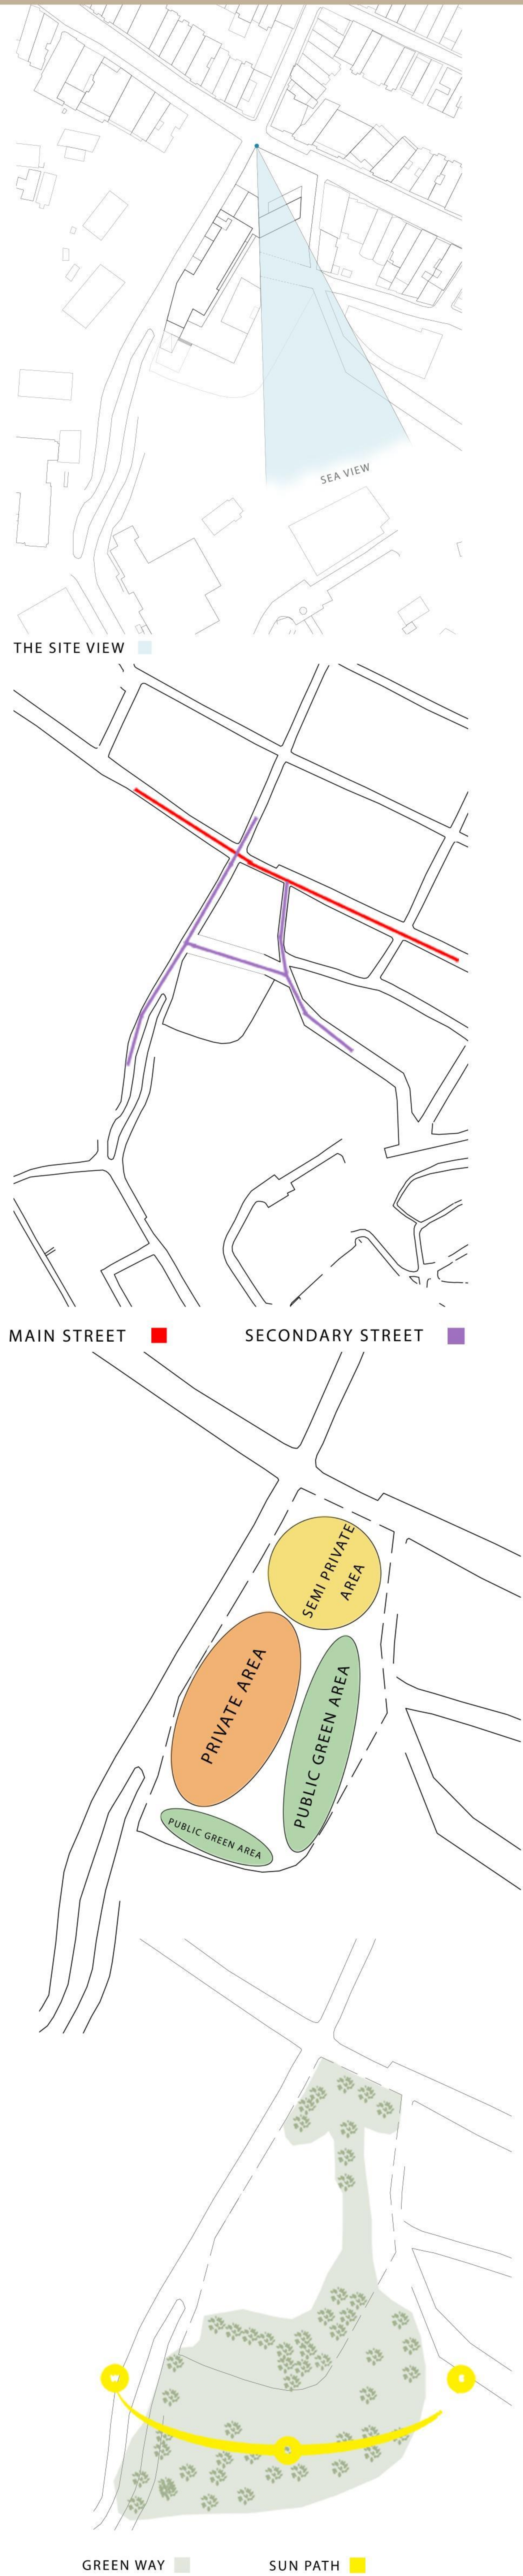


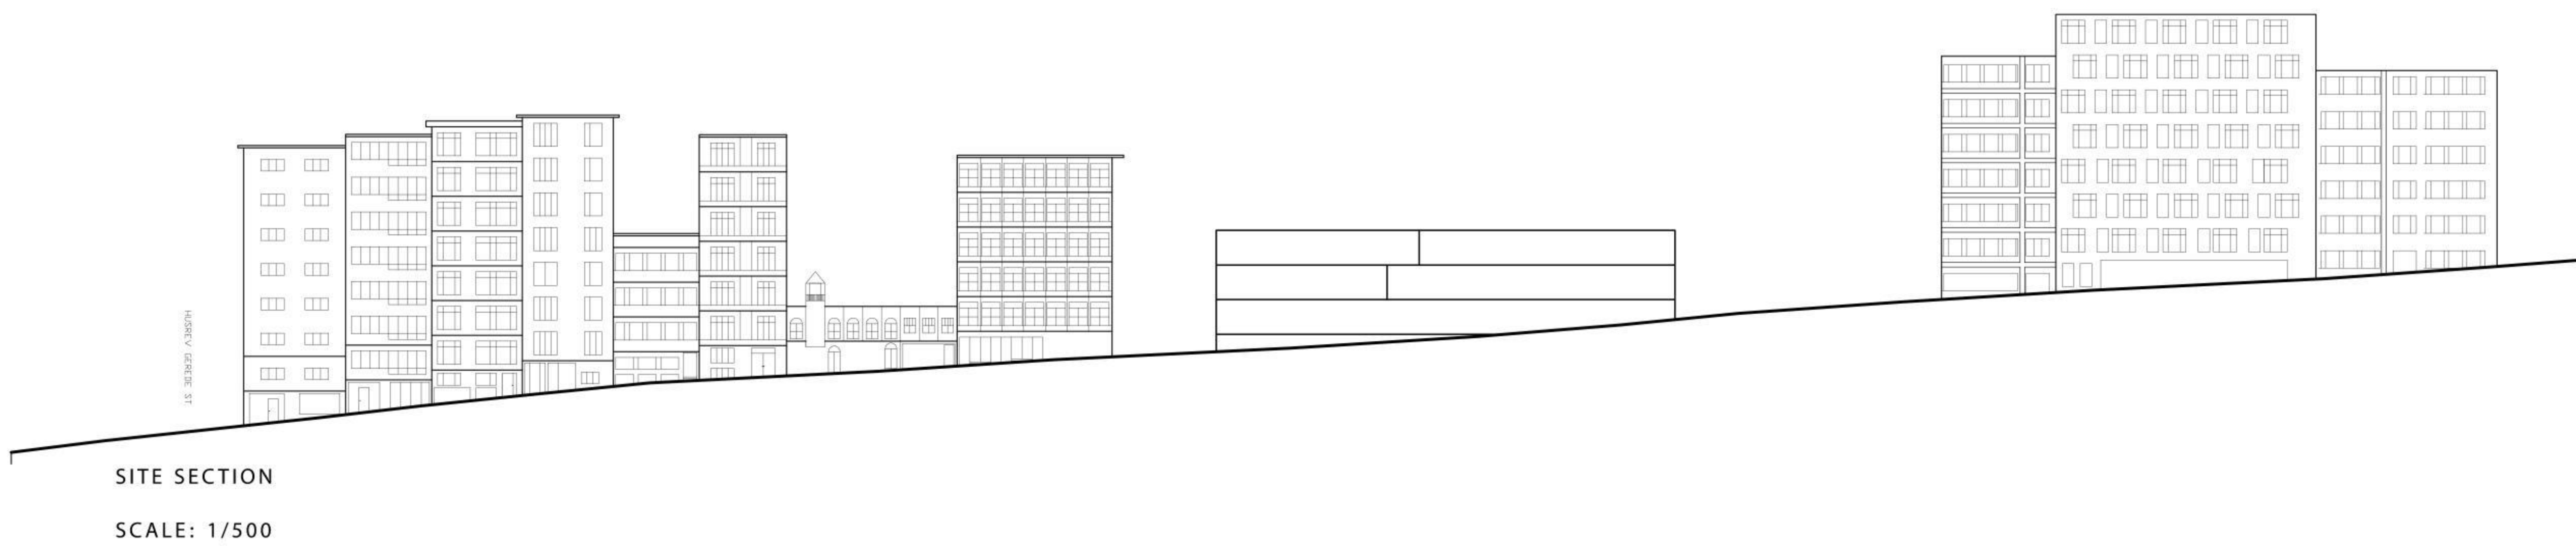

SITE PLAN SC: 1/500

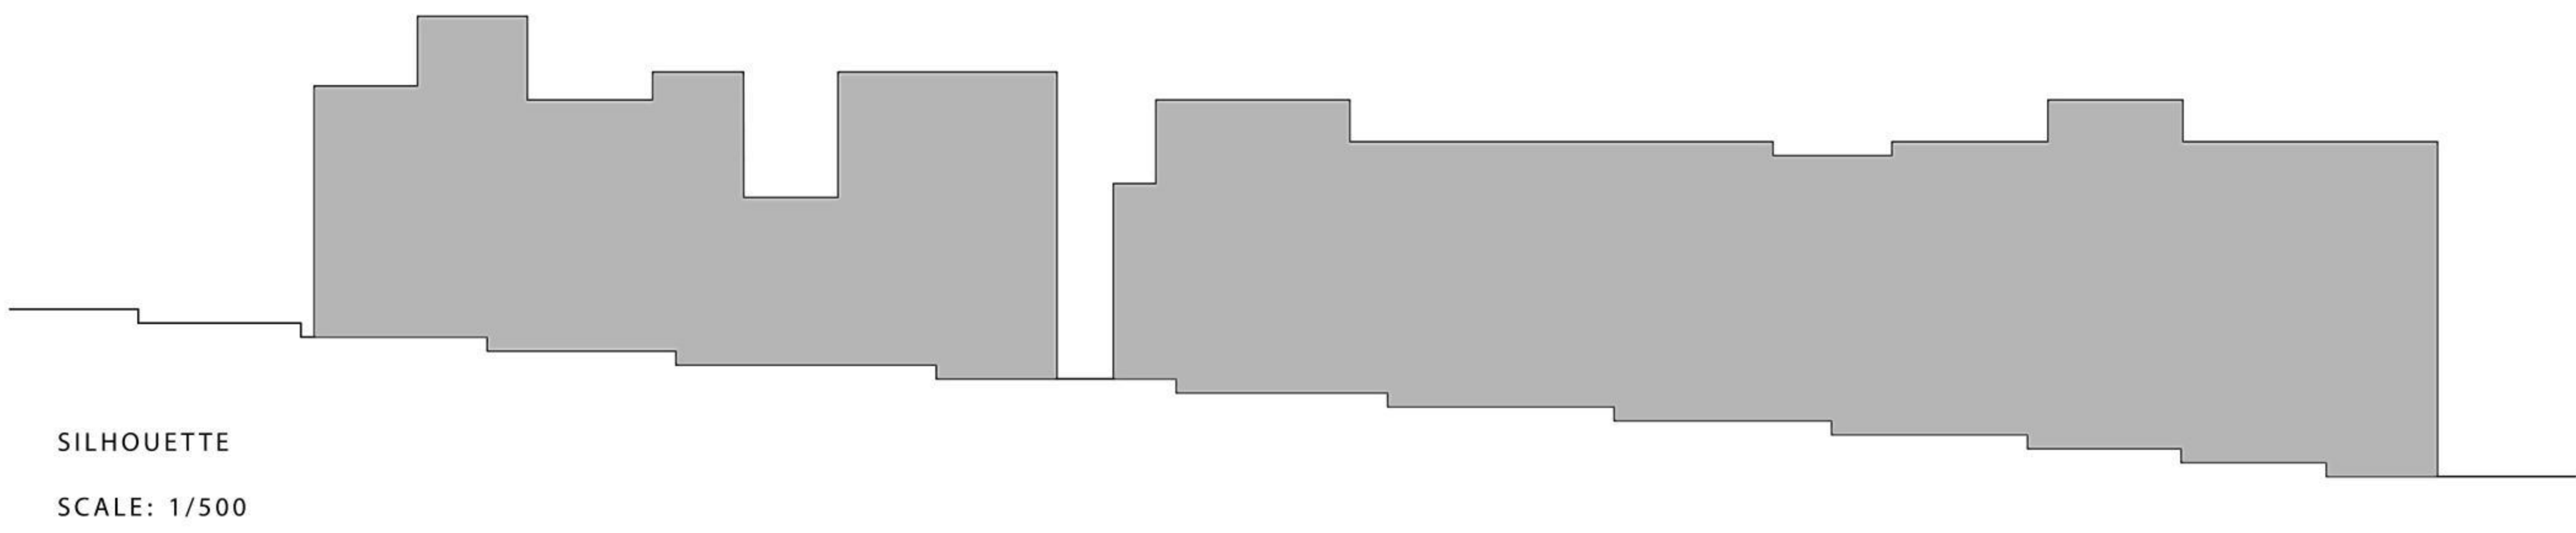






STEPS:

FIRST: A SOLID CUBE

SECOND: ALIGN WITH SURROUNDING
AND VIEW LINE

THIRD: MAKE VOID AND AVOID BLOCKING
VIEW BY PUTTING STAIRCASE

FOURTH: INCREASE FLOOR

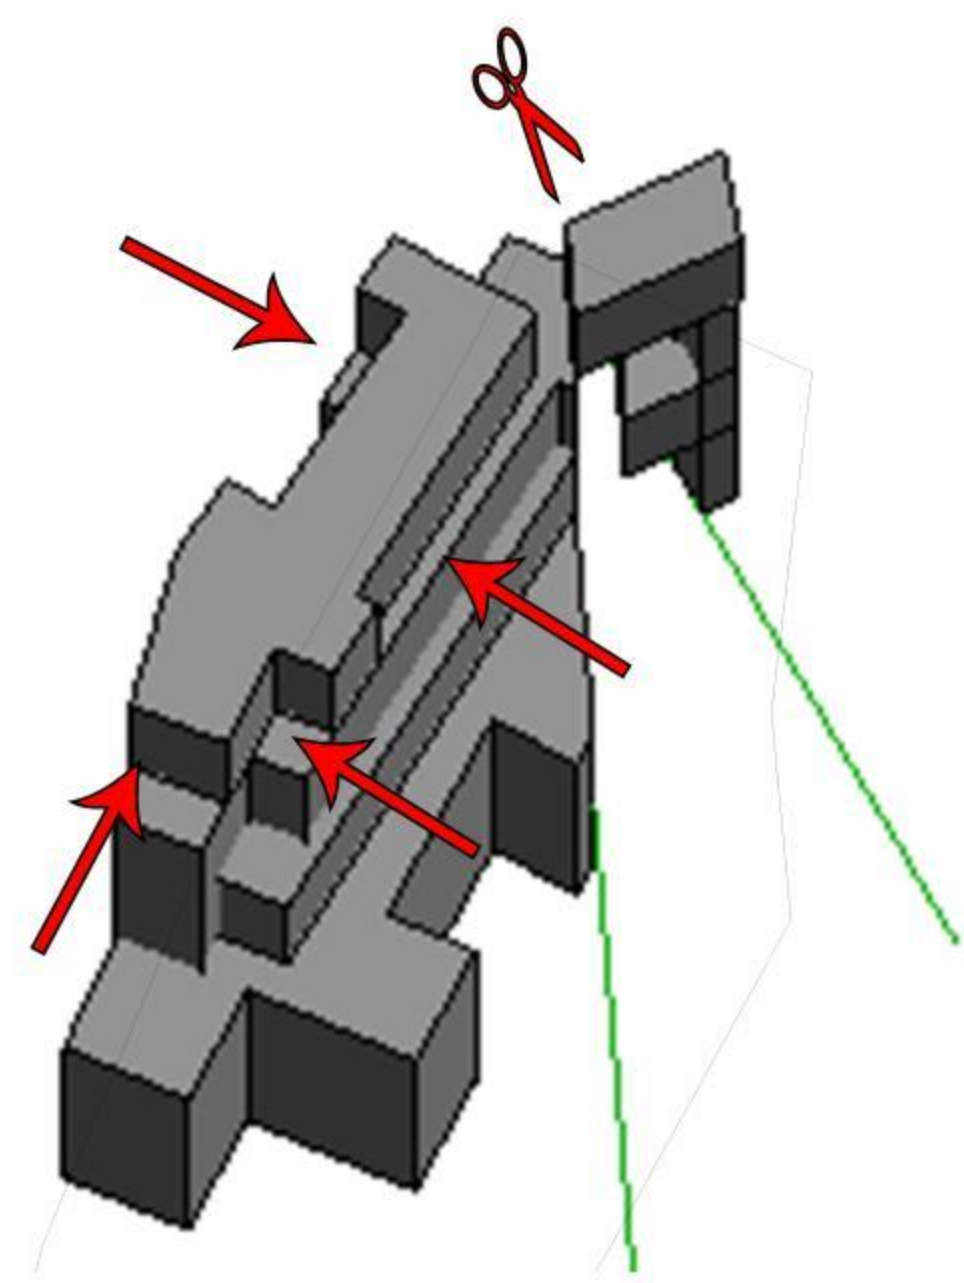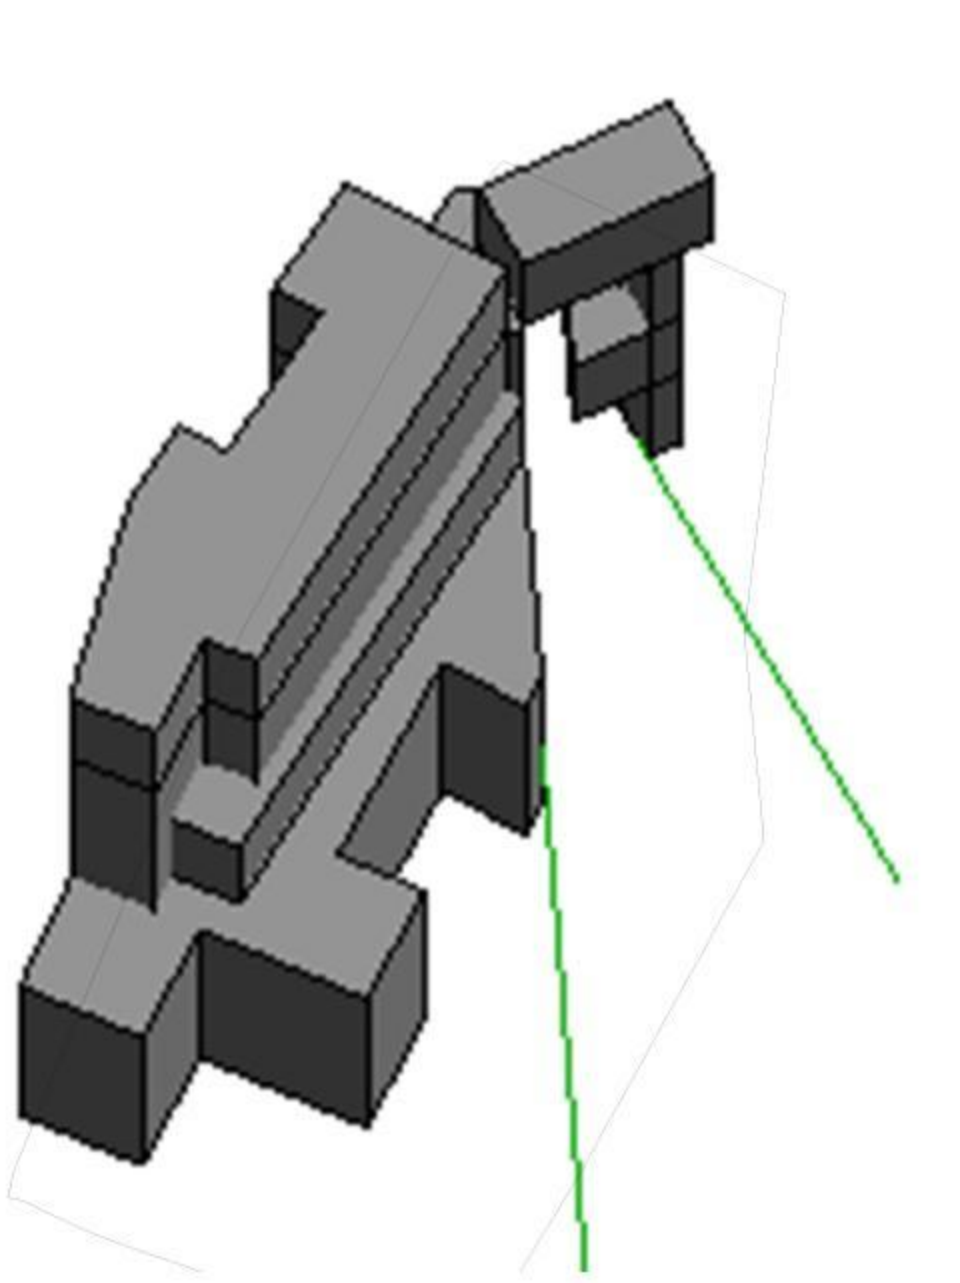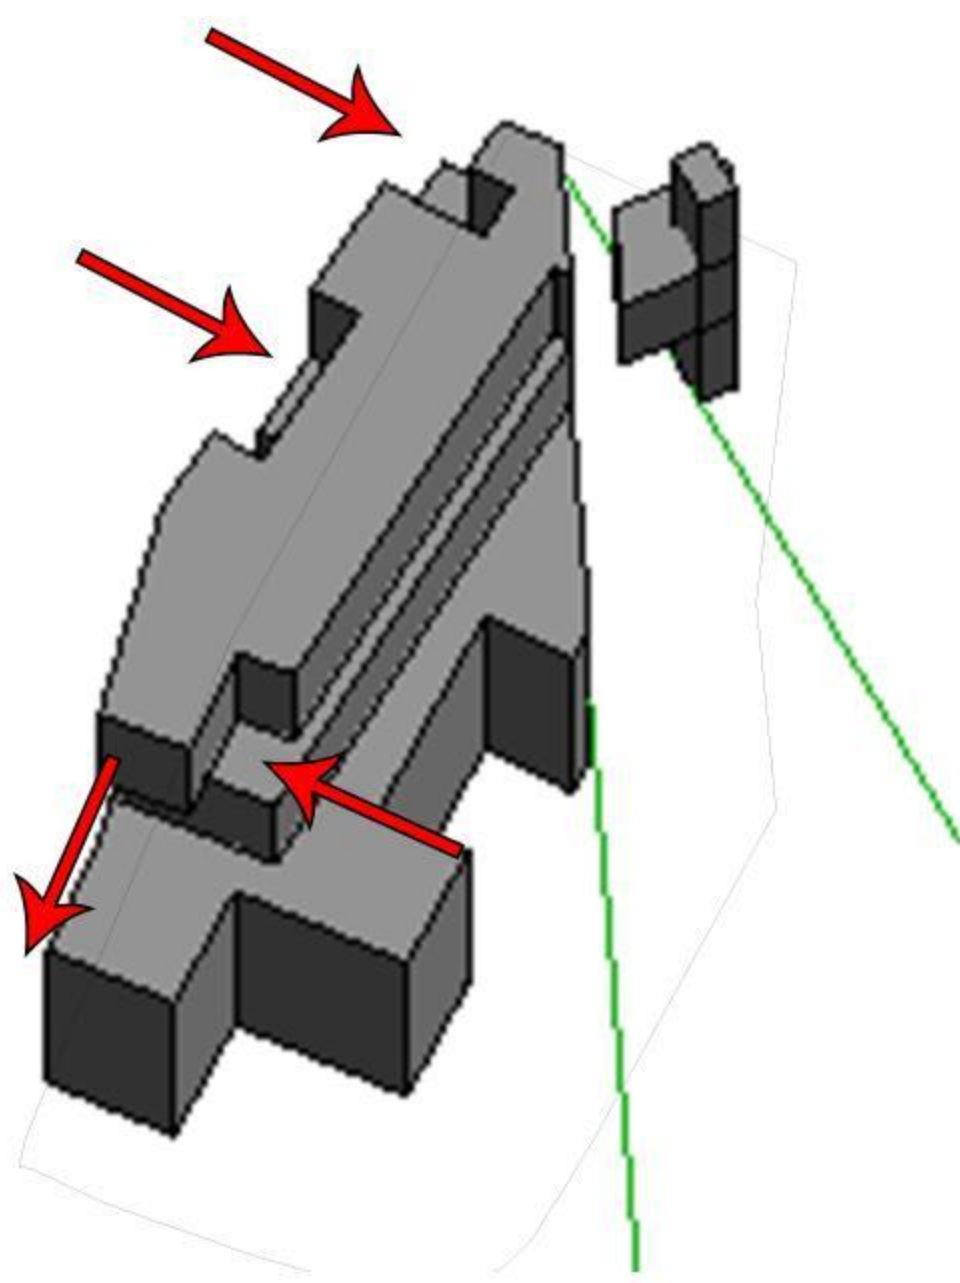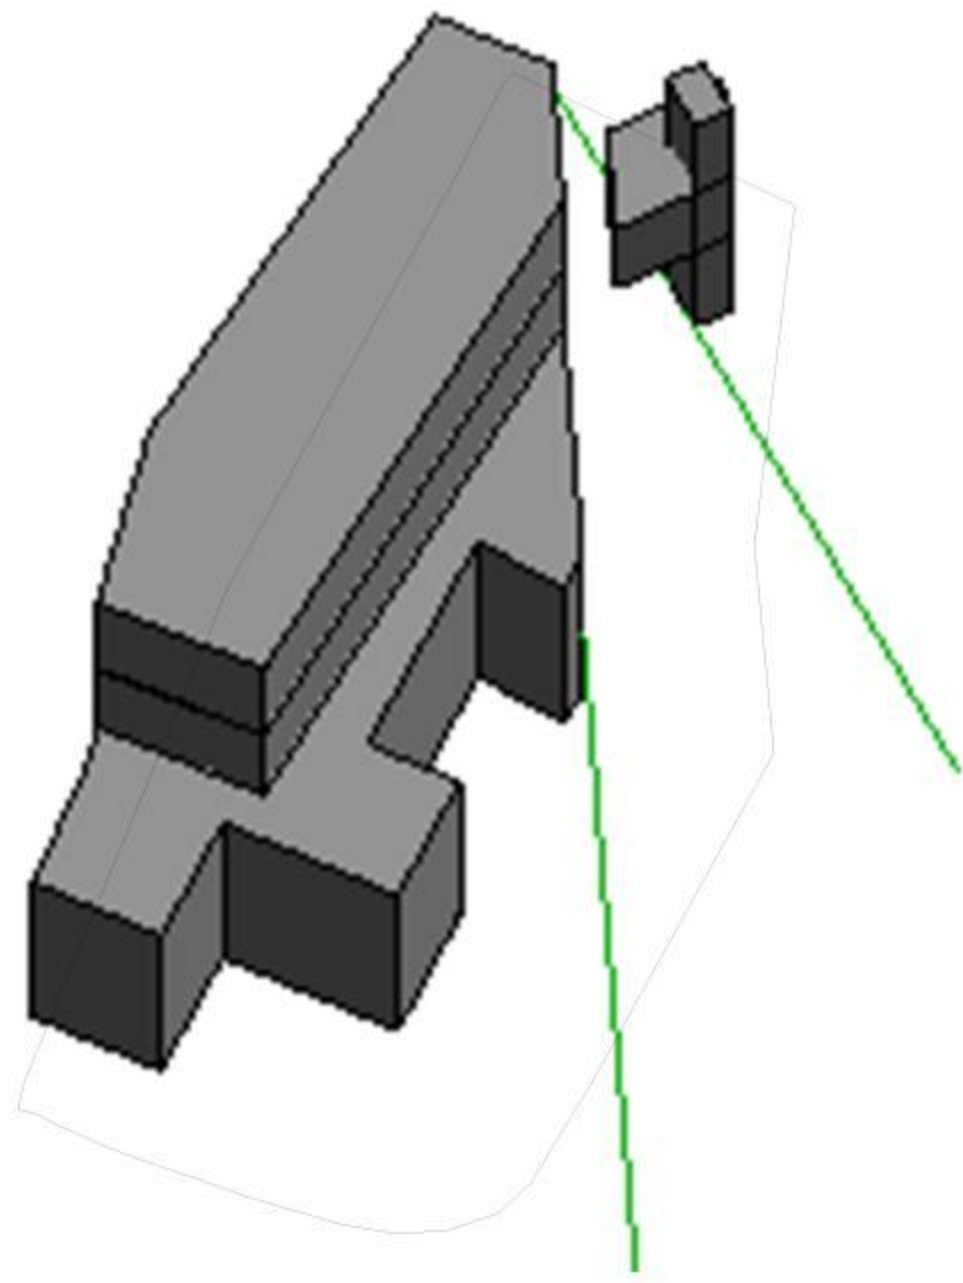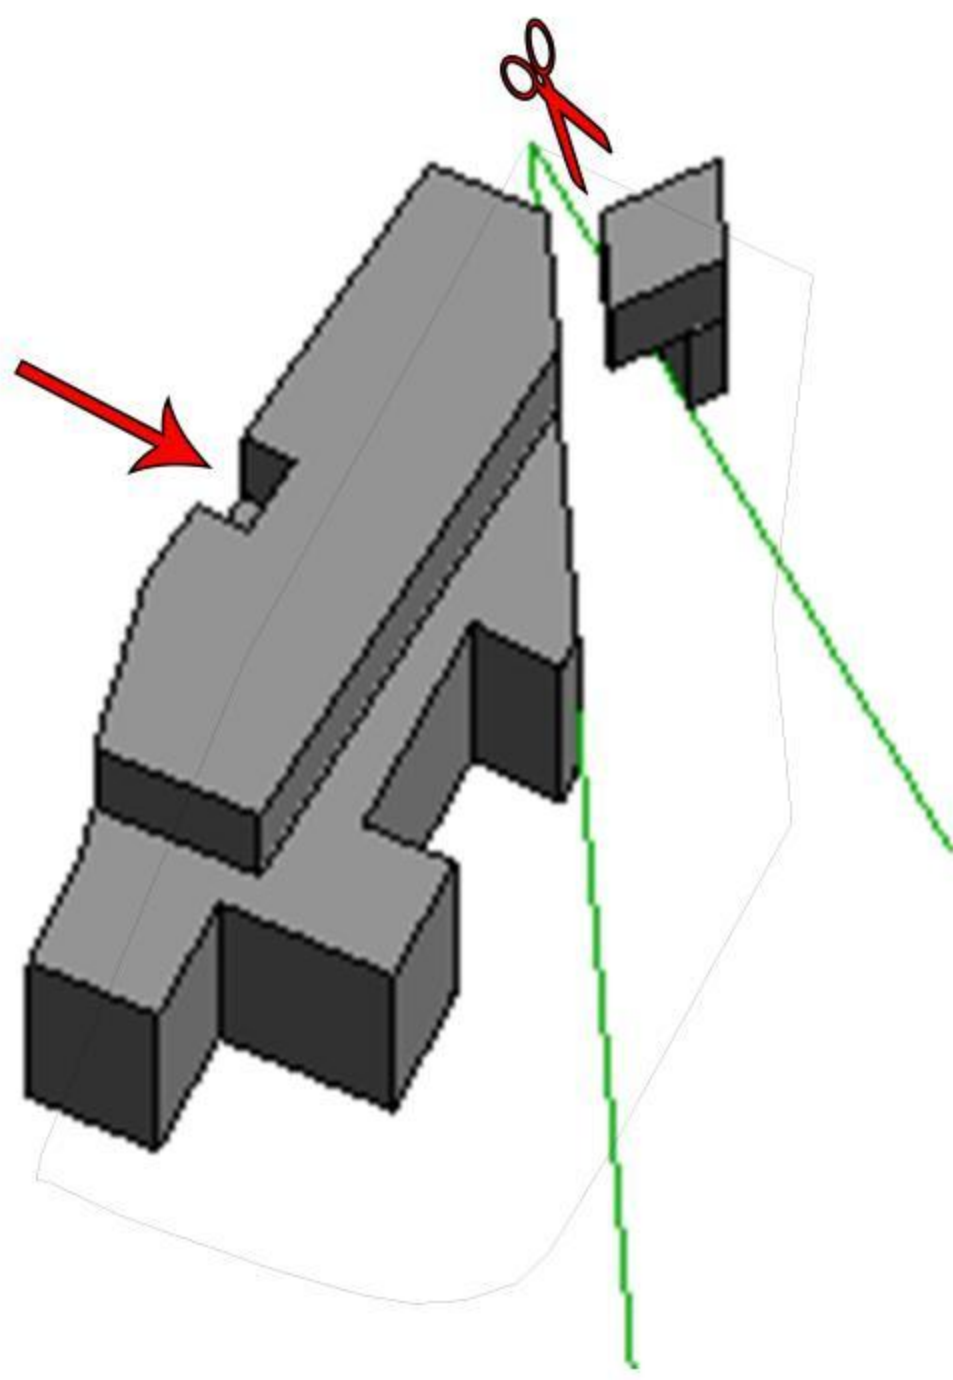


FIFTH: ALIGN WITH BOTTOM,
MAKE VOID FOR BEING LIGHT

SIXTH: INCREASE FLOOR




SEVENTH: MAKE VOID FOR BEING LIGHT,
PUSH FRONT FOR HAVING SEMI OPRN AREA

EIGHTH: INCREASE FLOOR


NINTH: MAKE VOID FOR MAKING
THE UNIT SO LIGHT

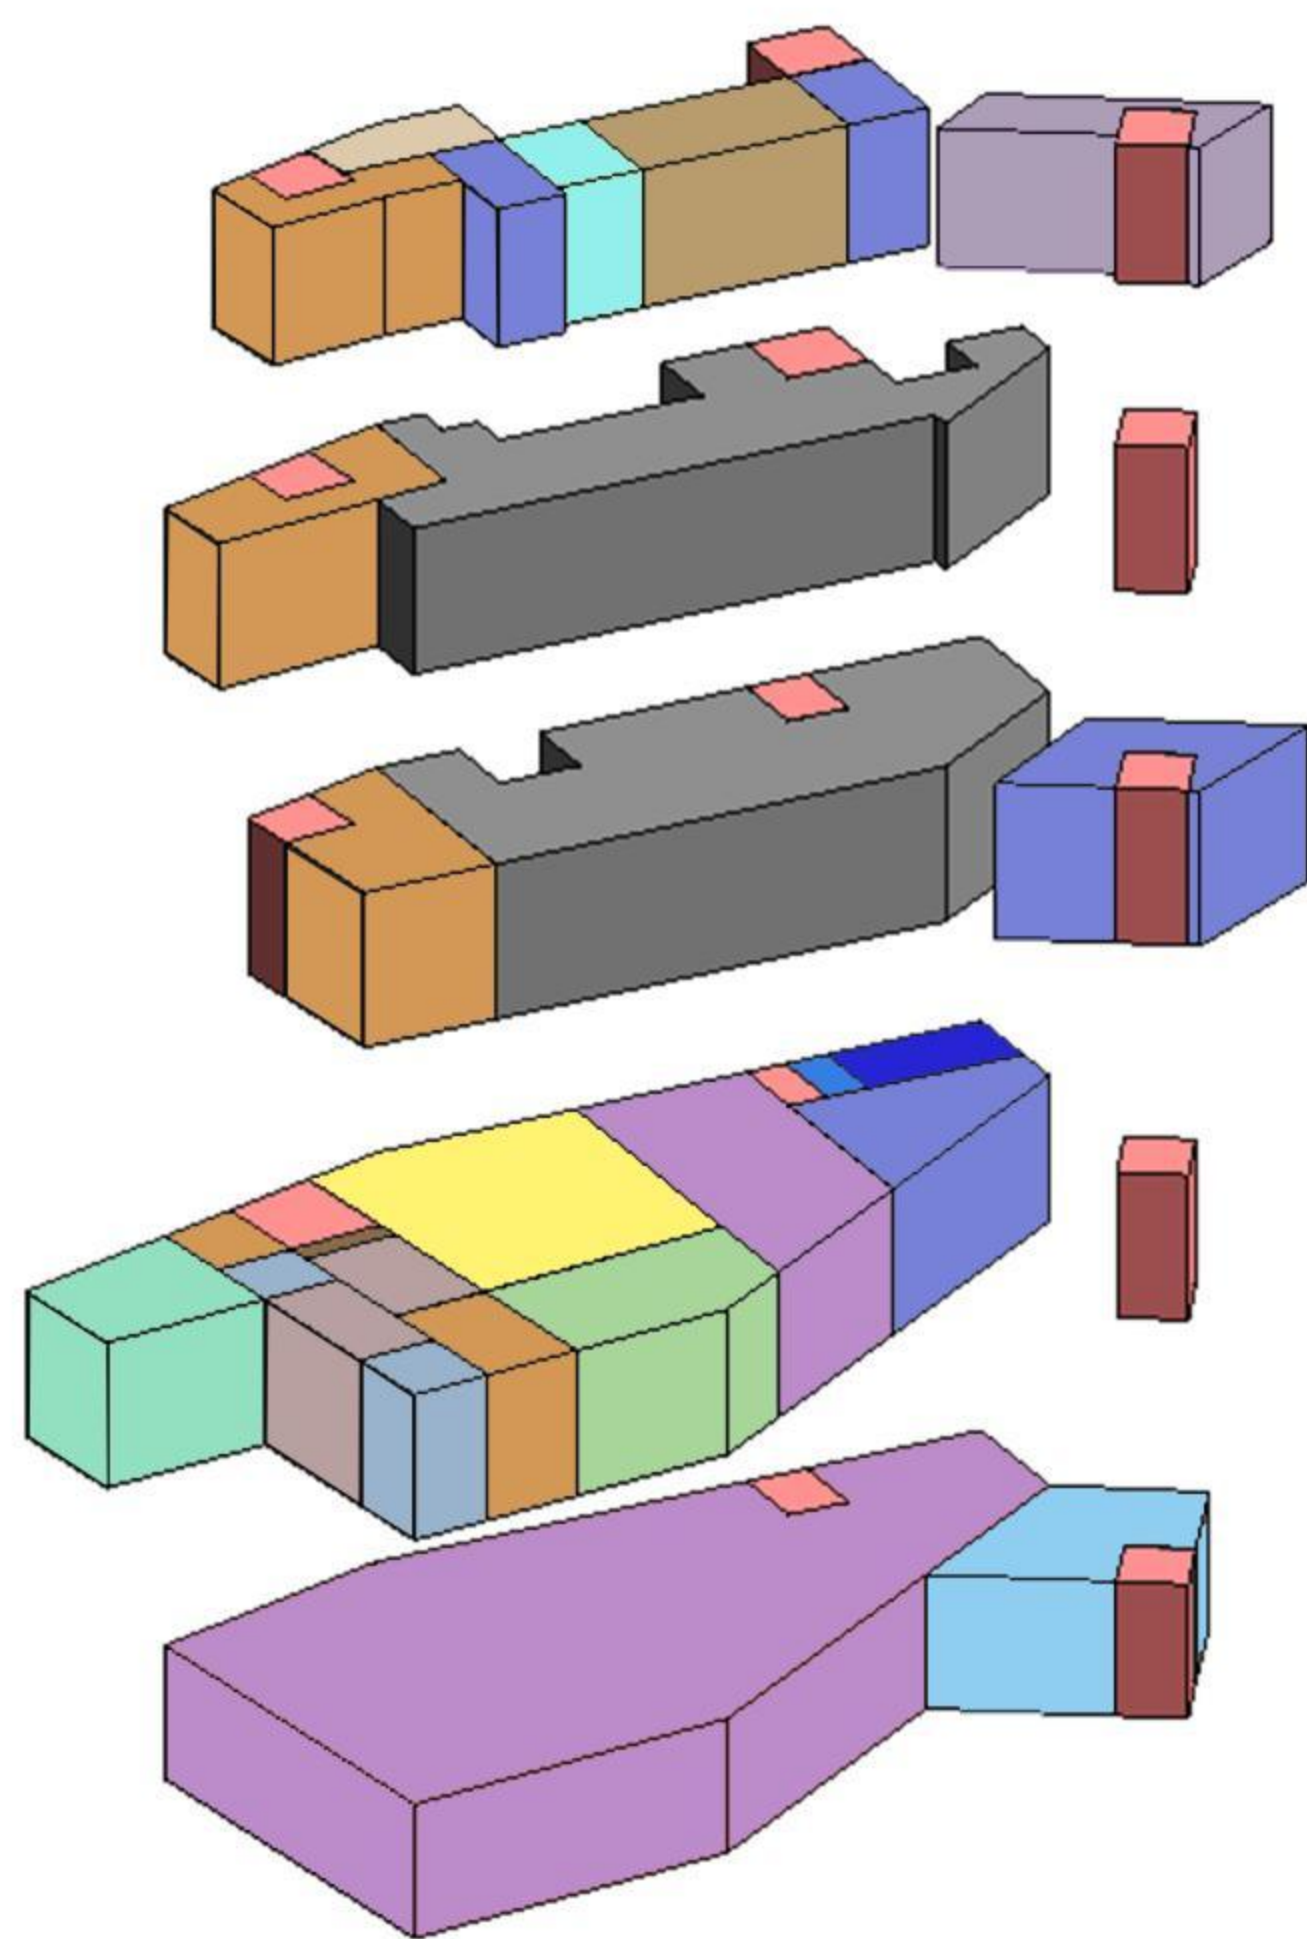

- PARKING
- SEMINAR
- STAIRCASE
- BEDROOMS
- COFFEE SHOP
- ART GALLERY
- PRINT ROOM
- GYM
- GARDEN
- LAUNDRY
- ADMINISTRATION
- KITCHEN AND DINING ROOM
- LIVING ROOM
- EXHIBITION ROOM
- LIBRARY
- STUDY ROOM
- WORKSHOP

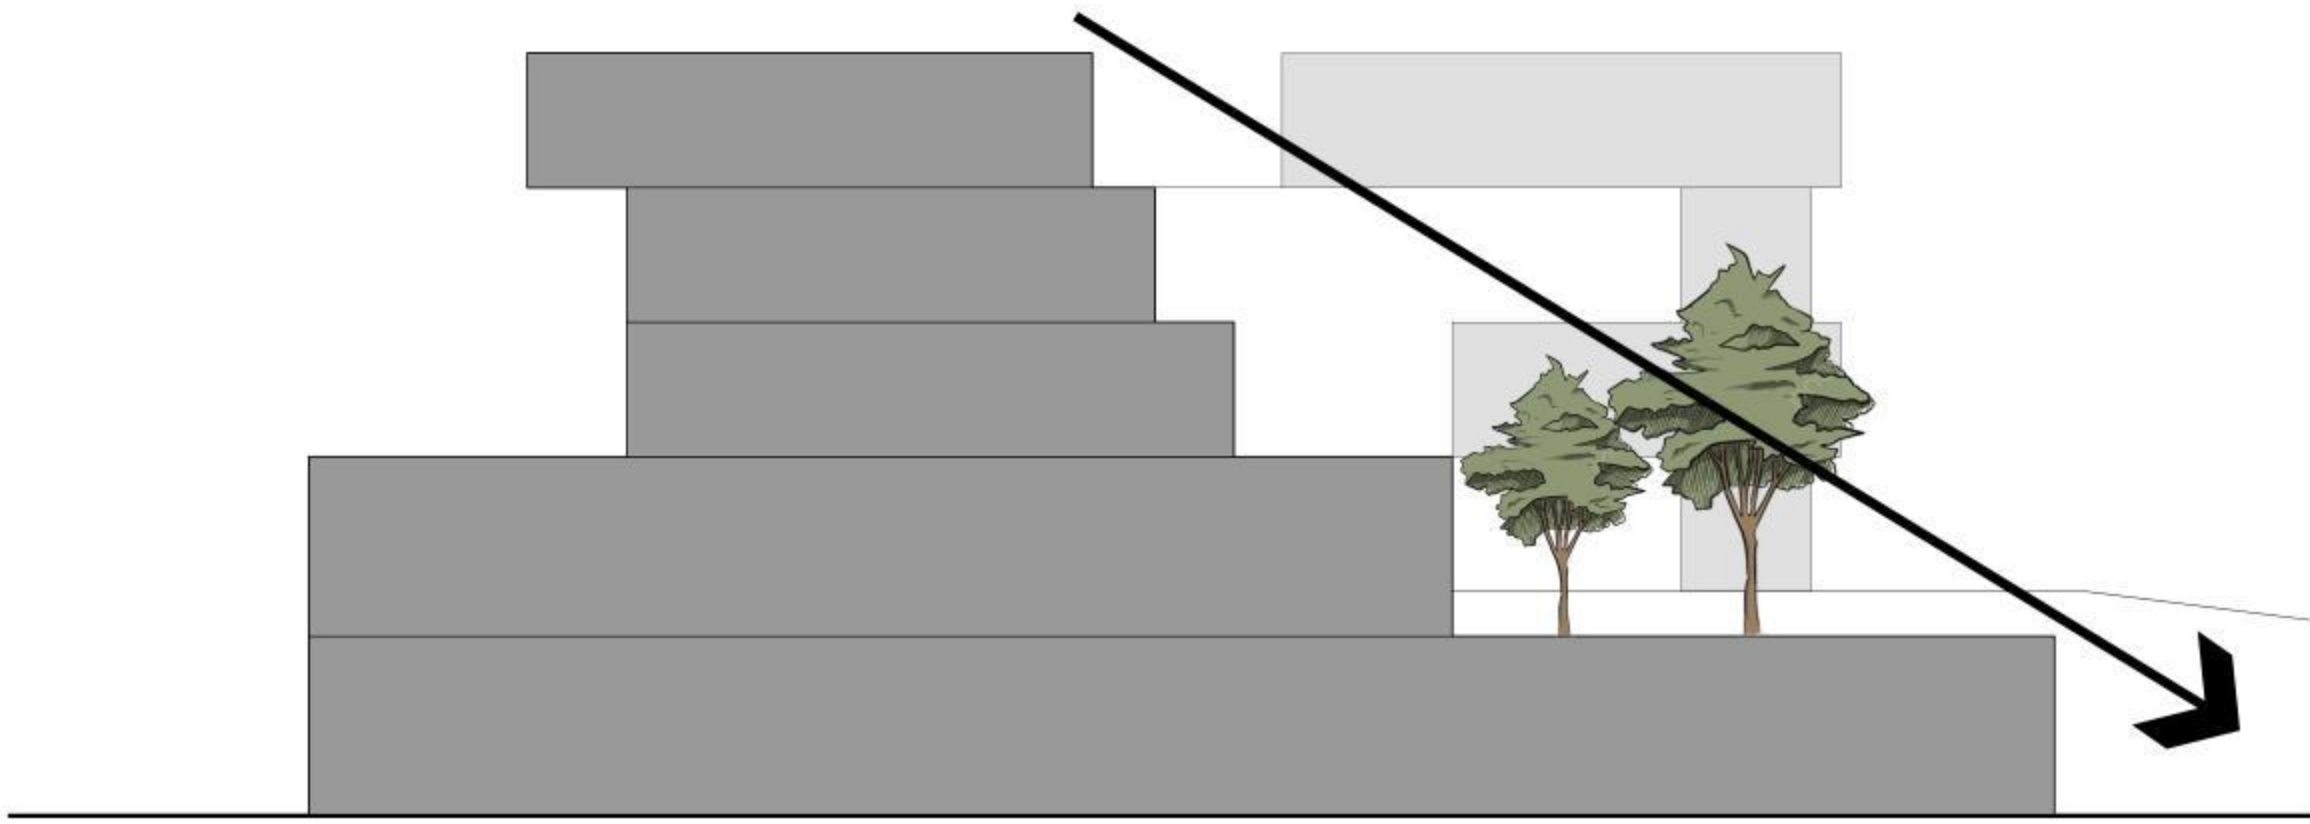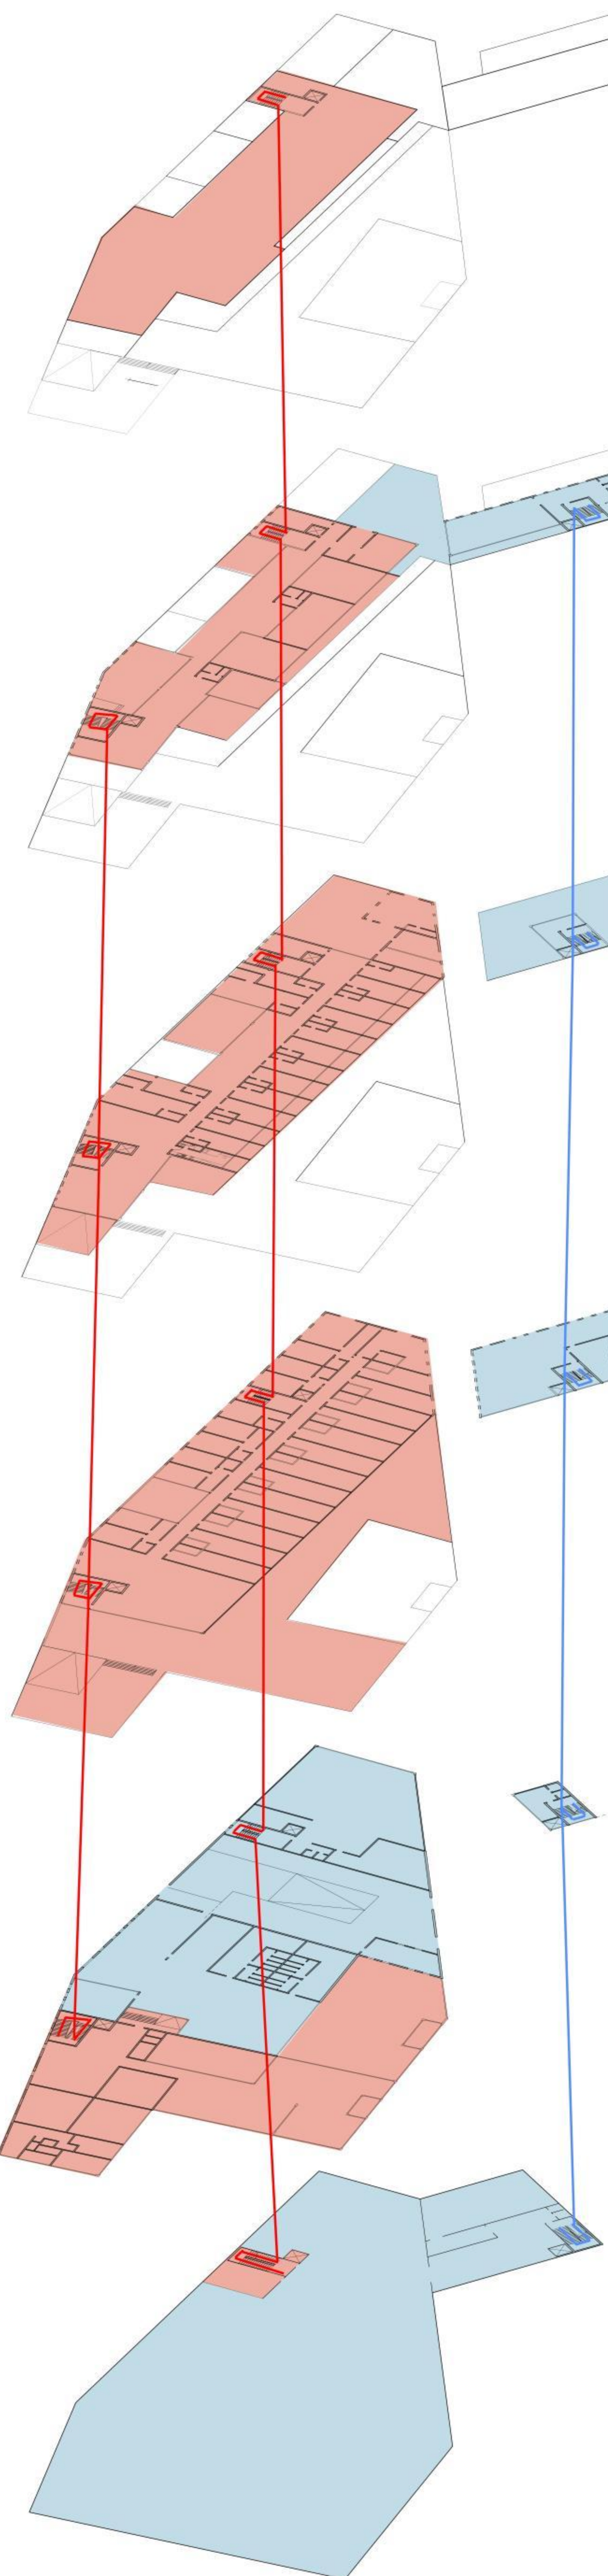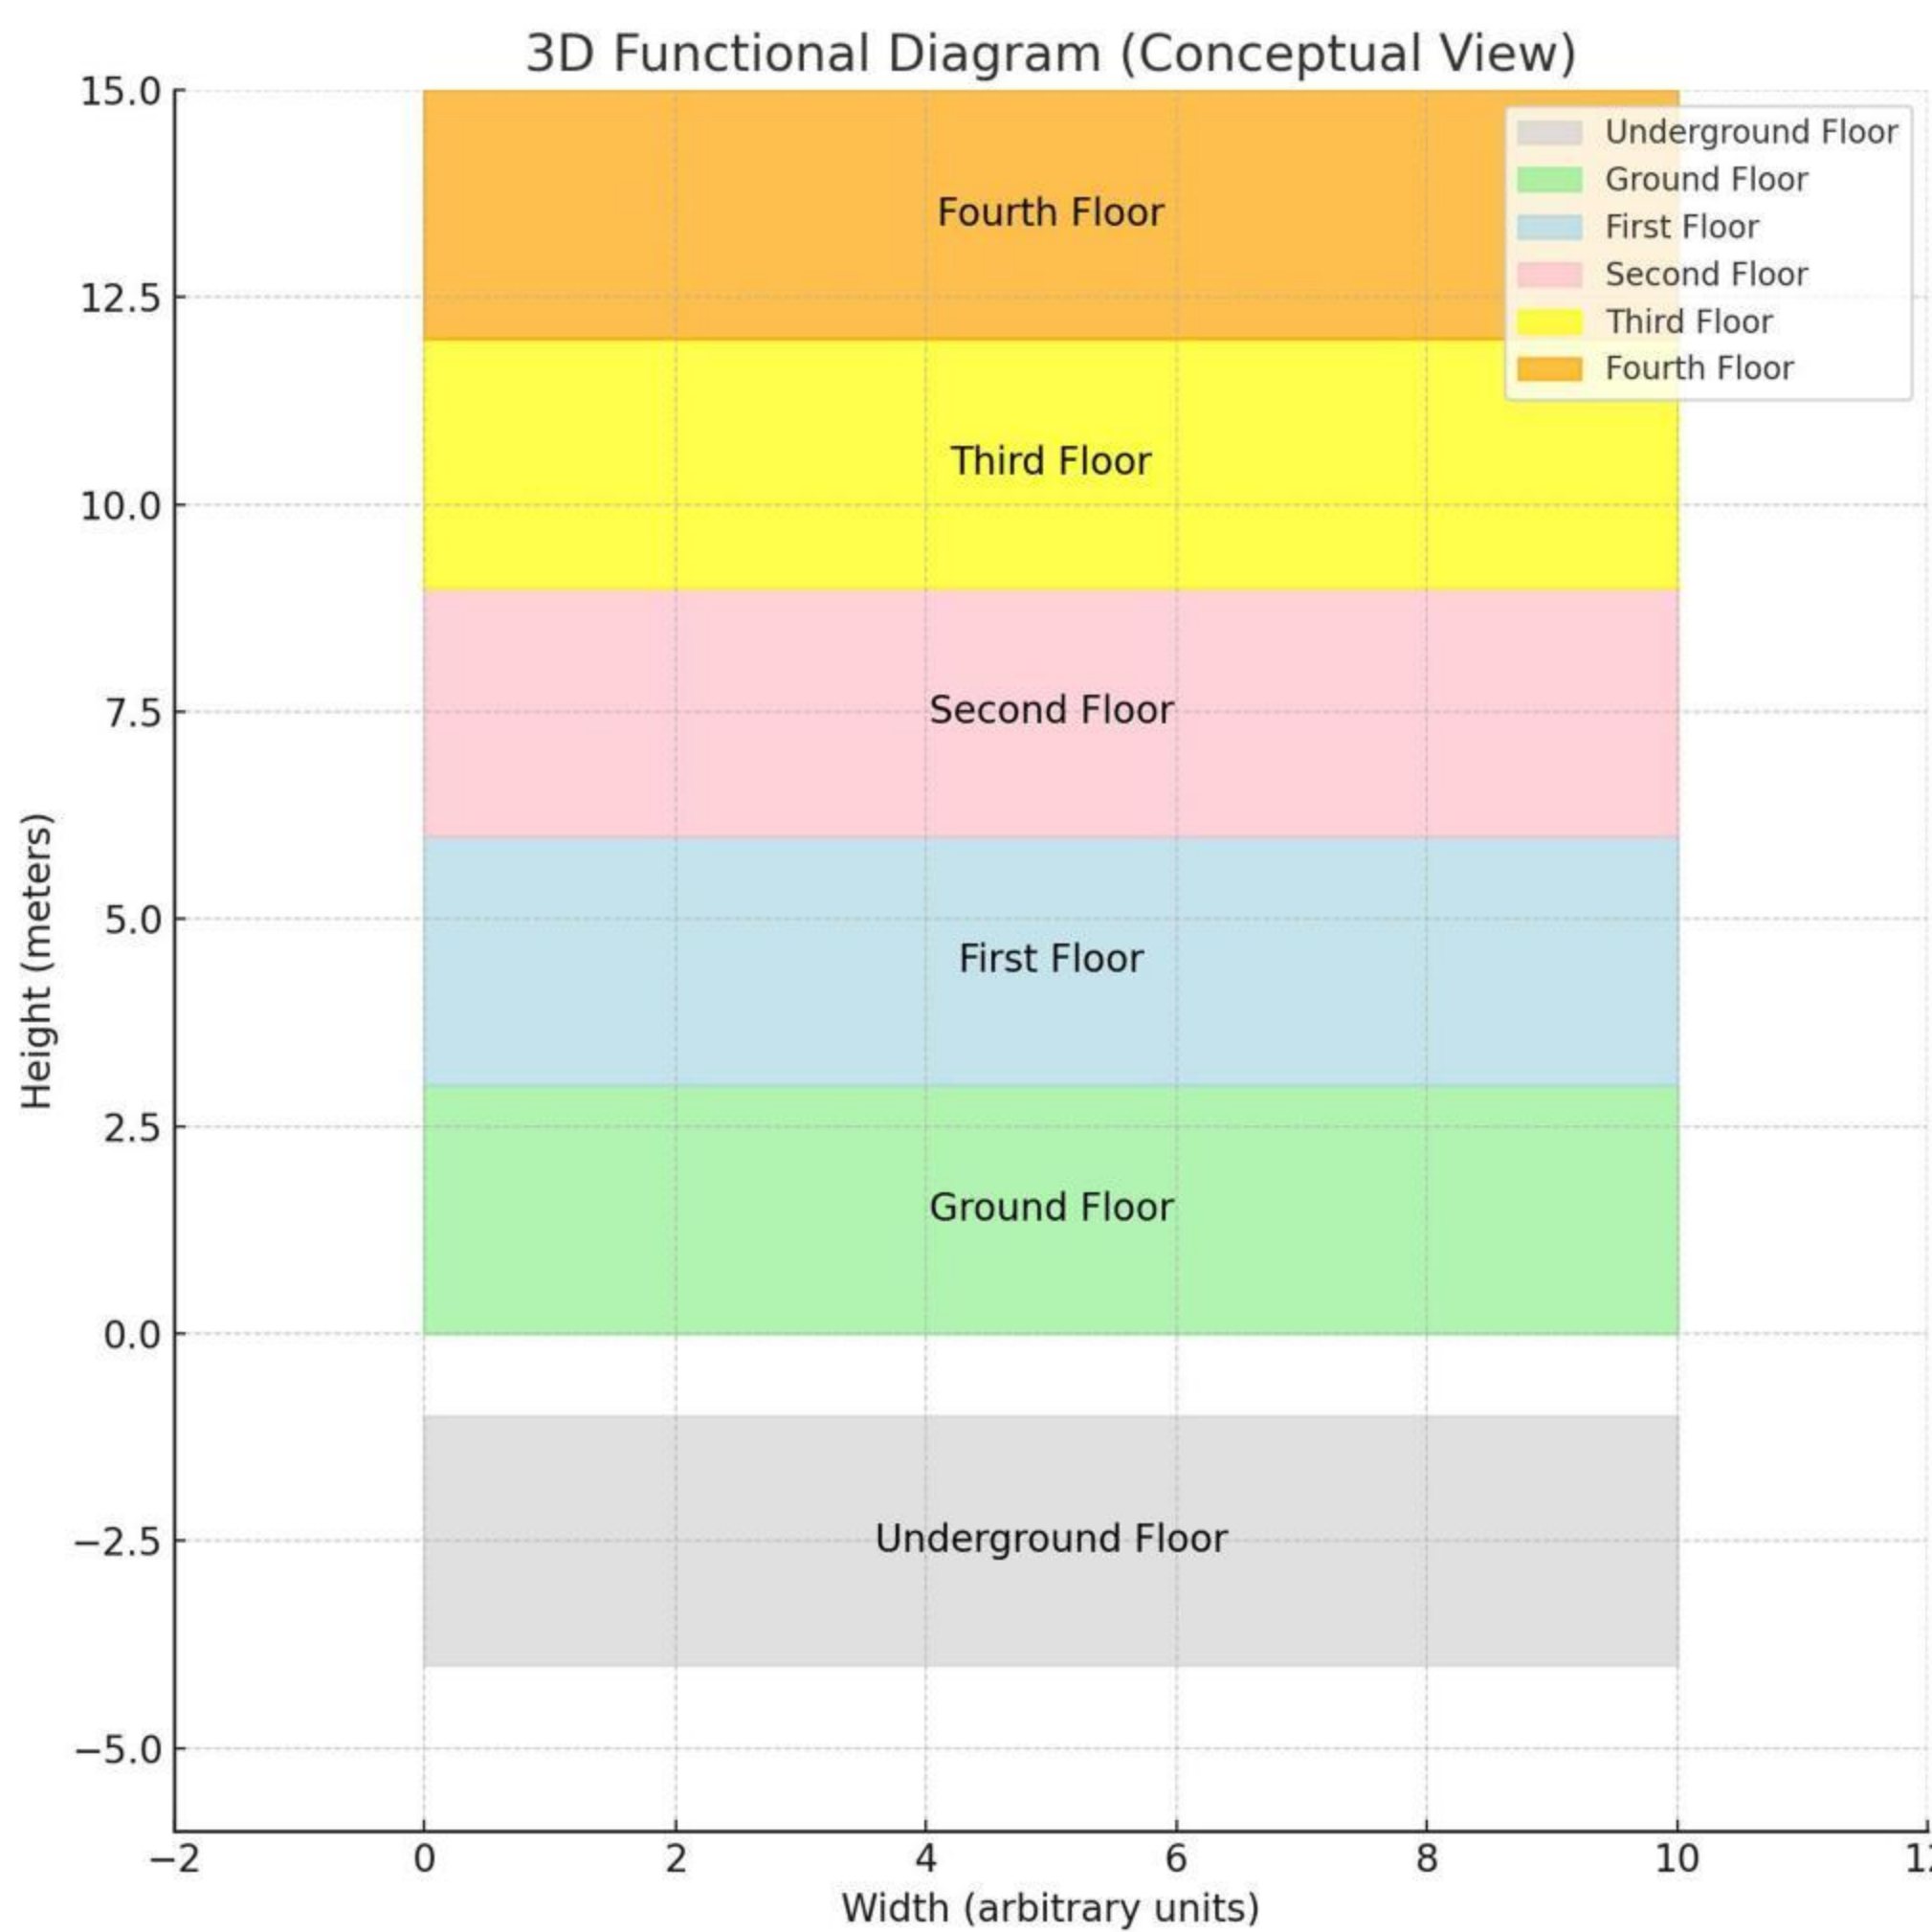





DIFFRENT LEVEL DEPENDS ON TOPOGRAPHY

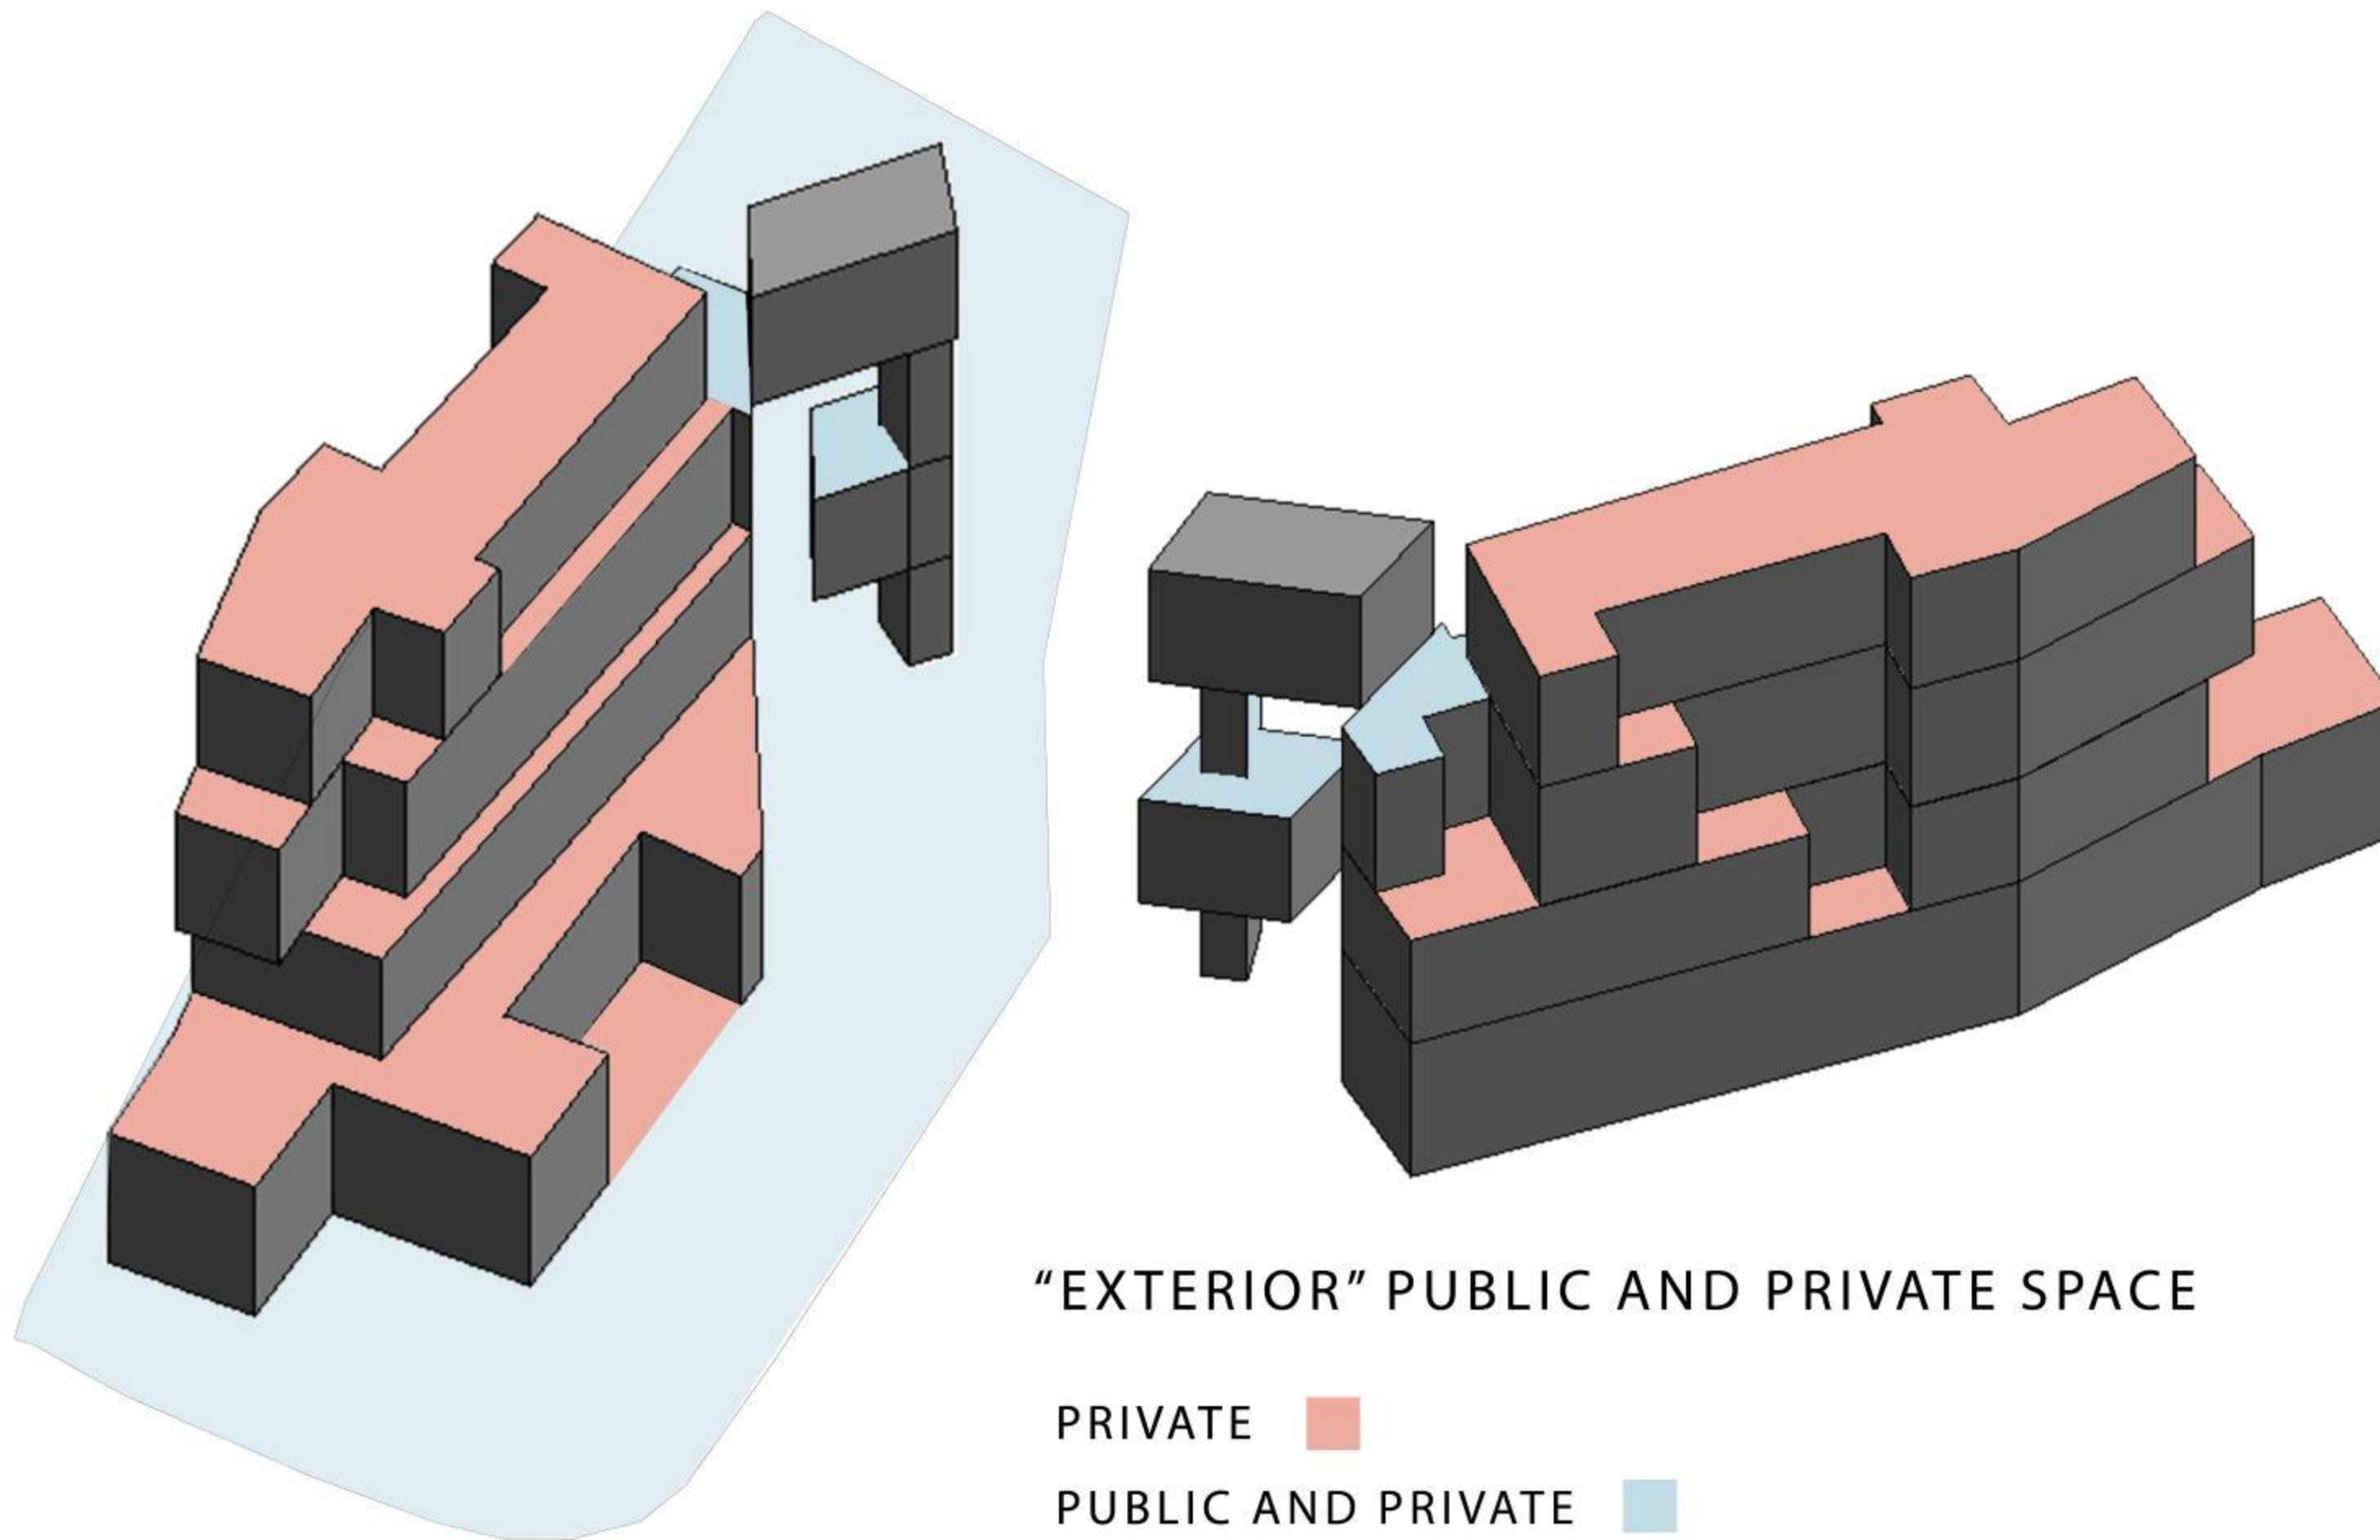

"EXTERIOR" PUBLIC AND PRIVATE SPACE


PRIVATE
PUBLIC AND PRIVATE

WINDOW
COVER
EXAMPLE

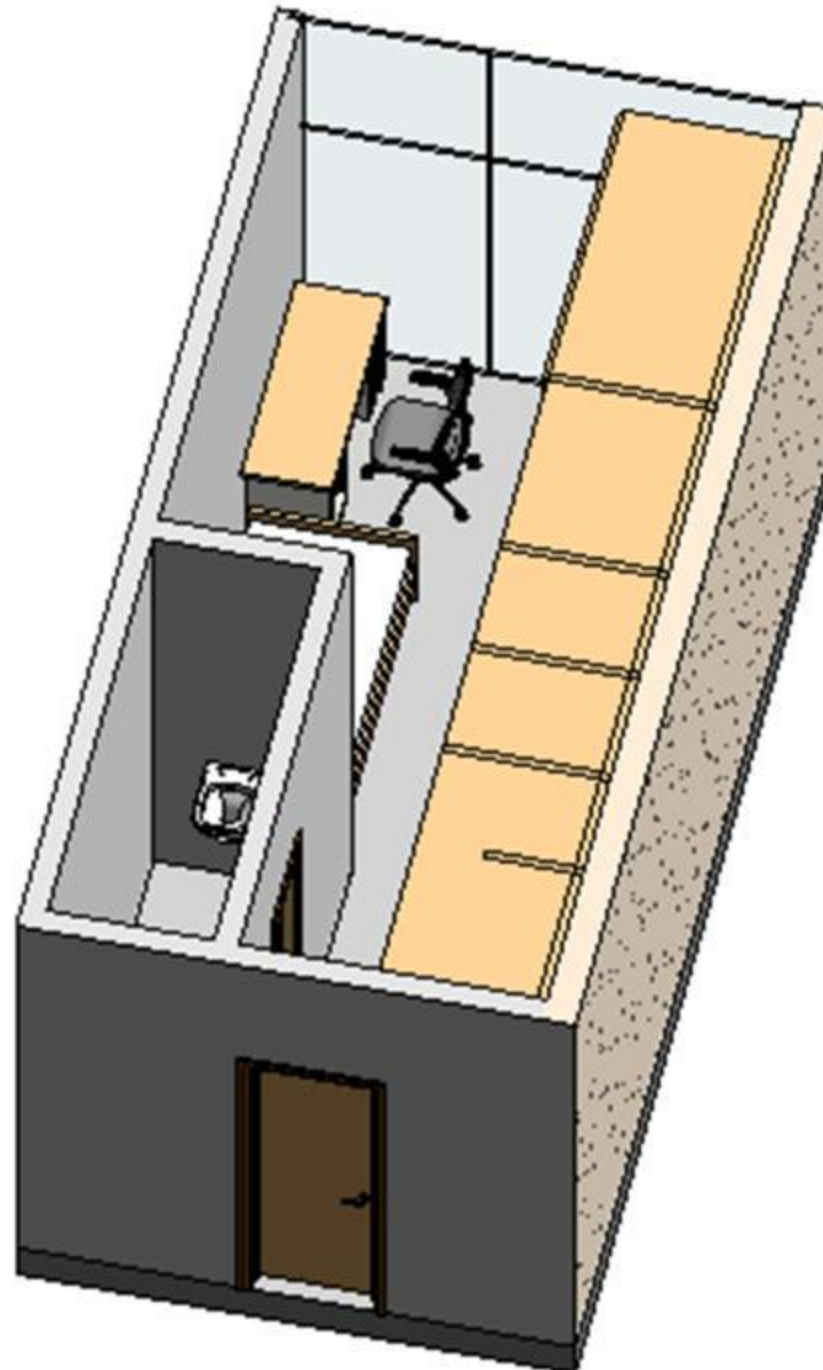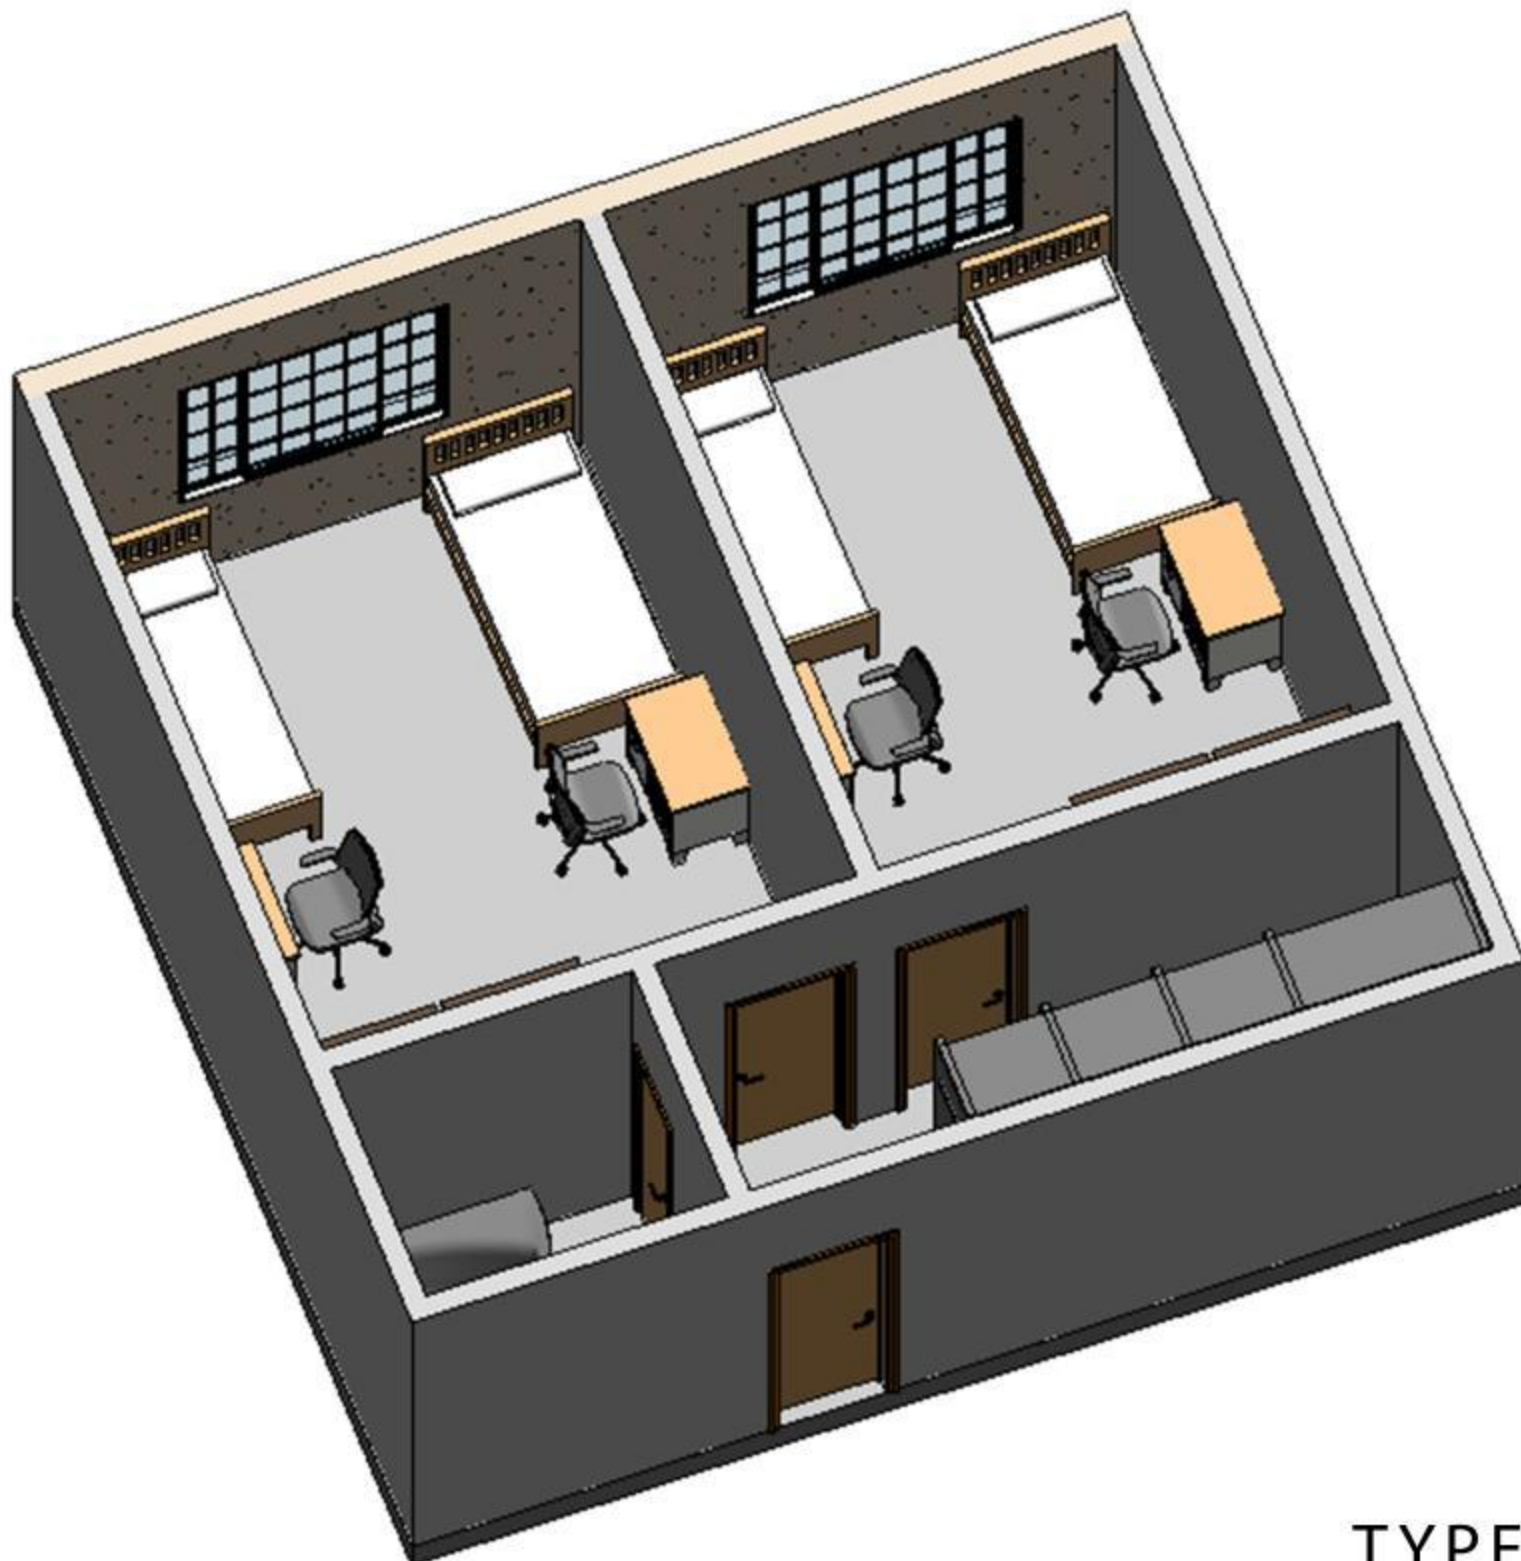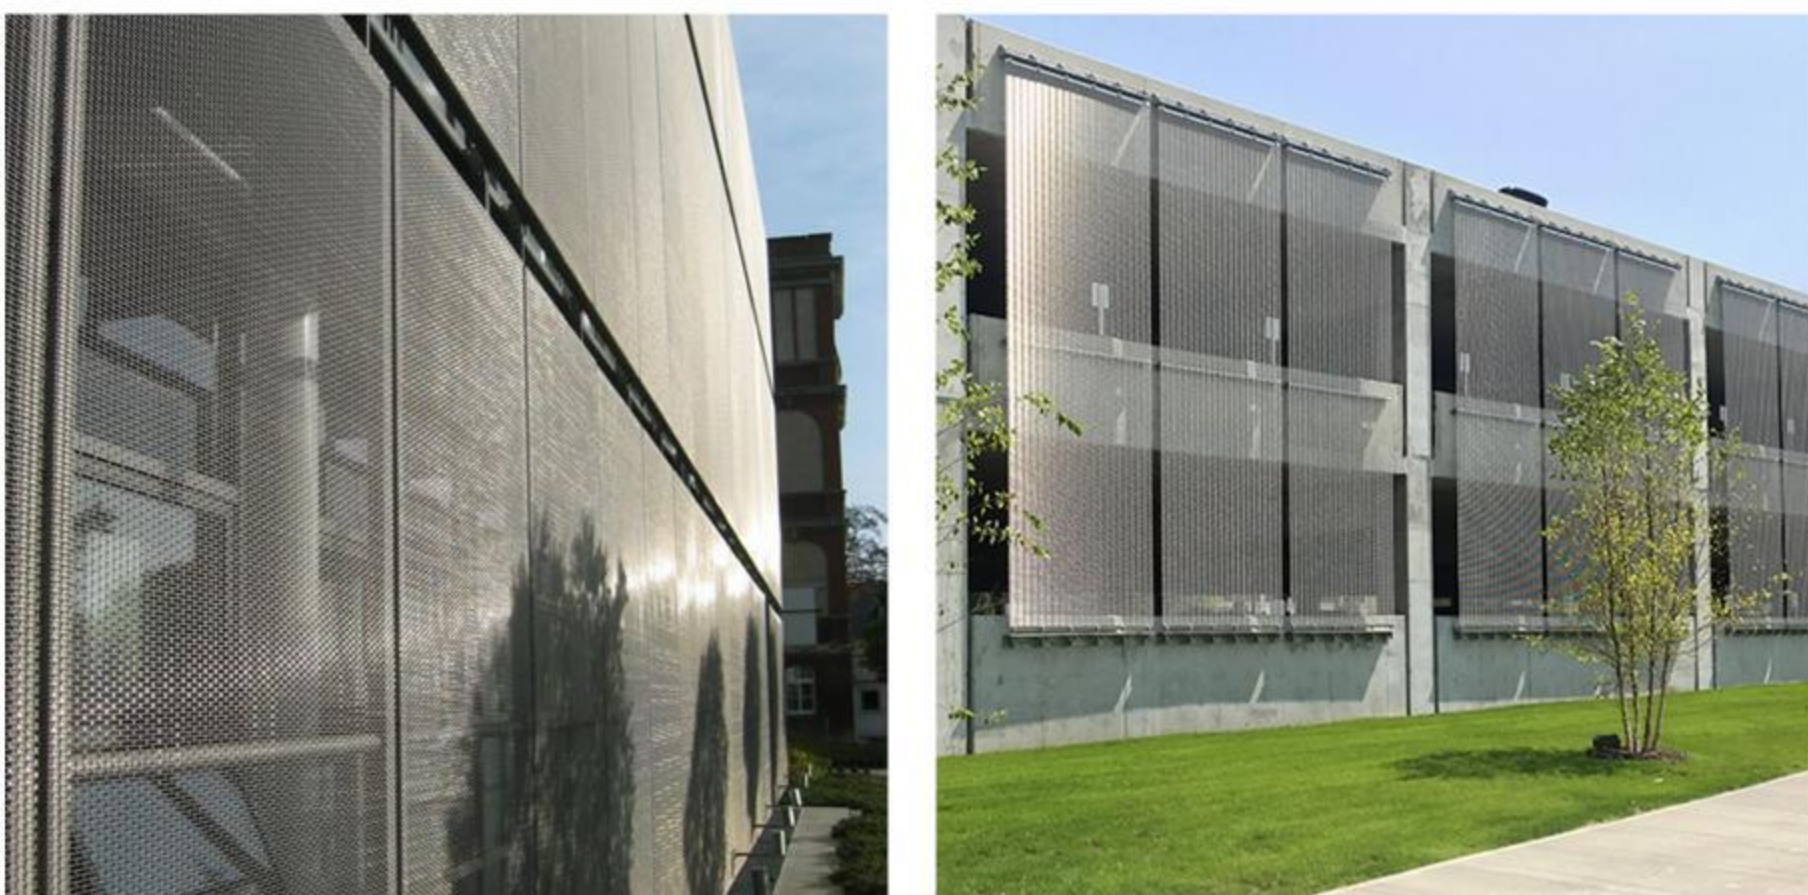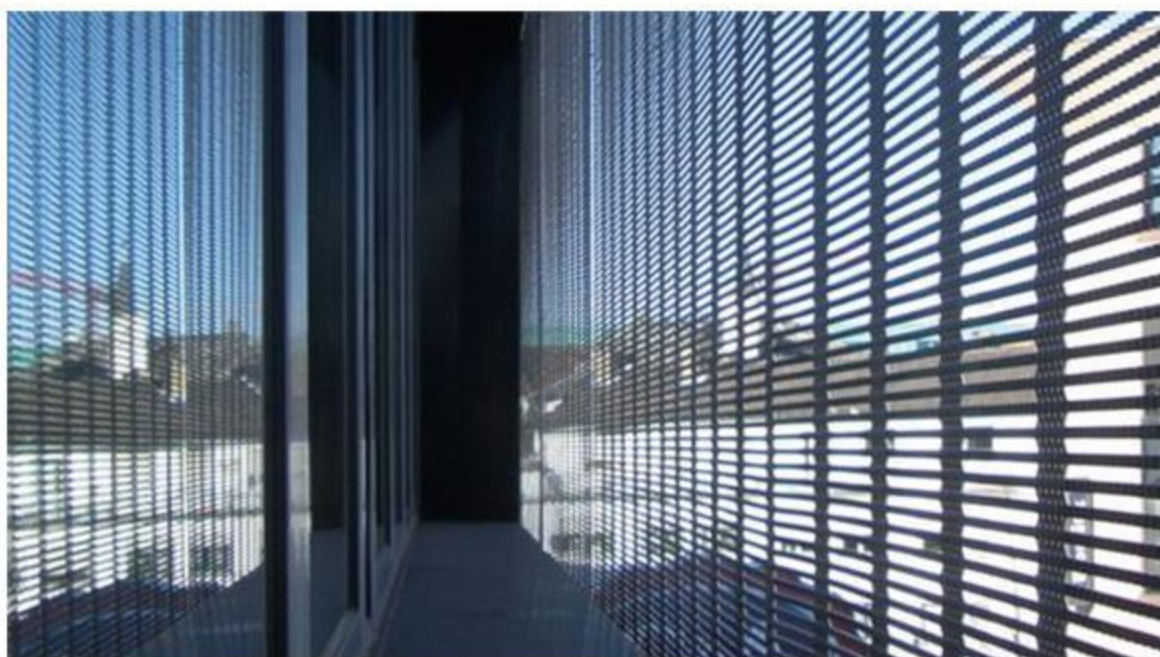


TYPE OF ROOM

"INTERIOR" PUBLIC AND PRIVATE SPACE
PRIVATE
PUBLIC AND PRIVATE



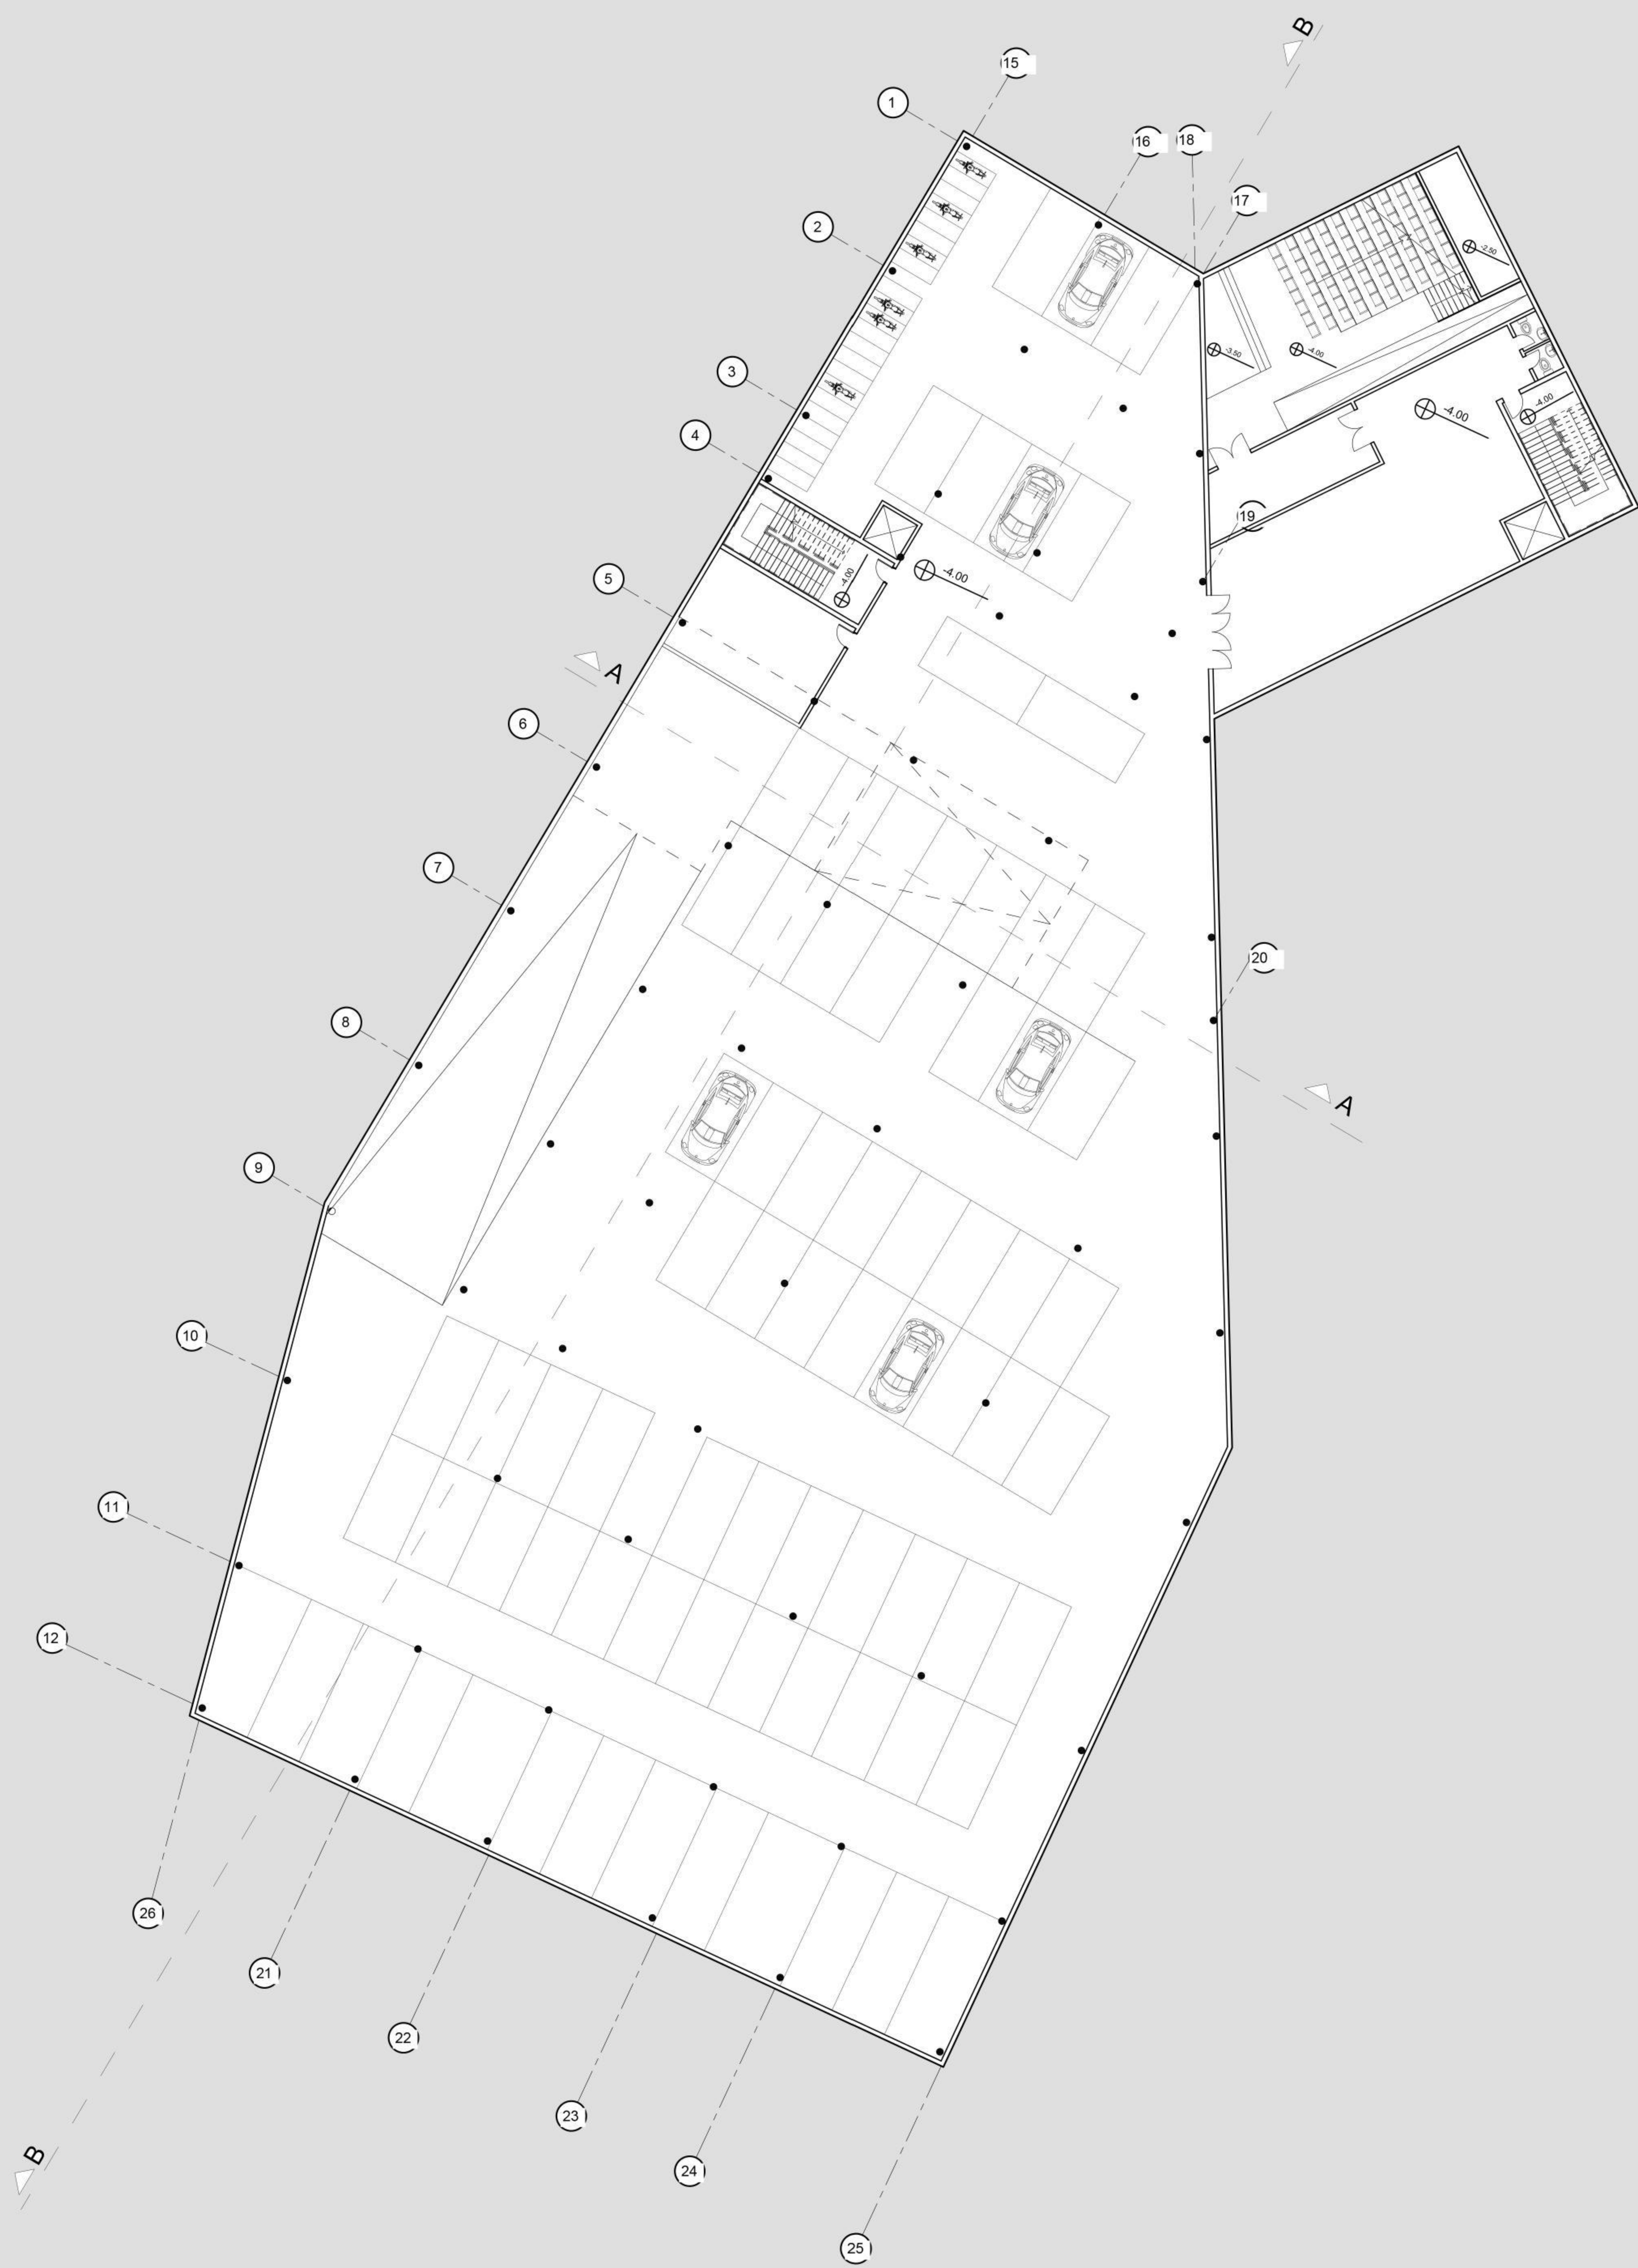









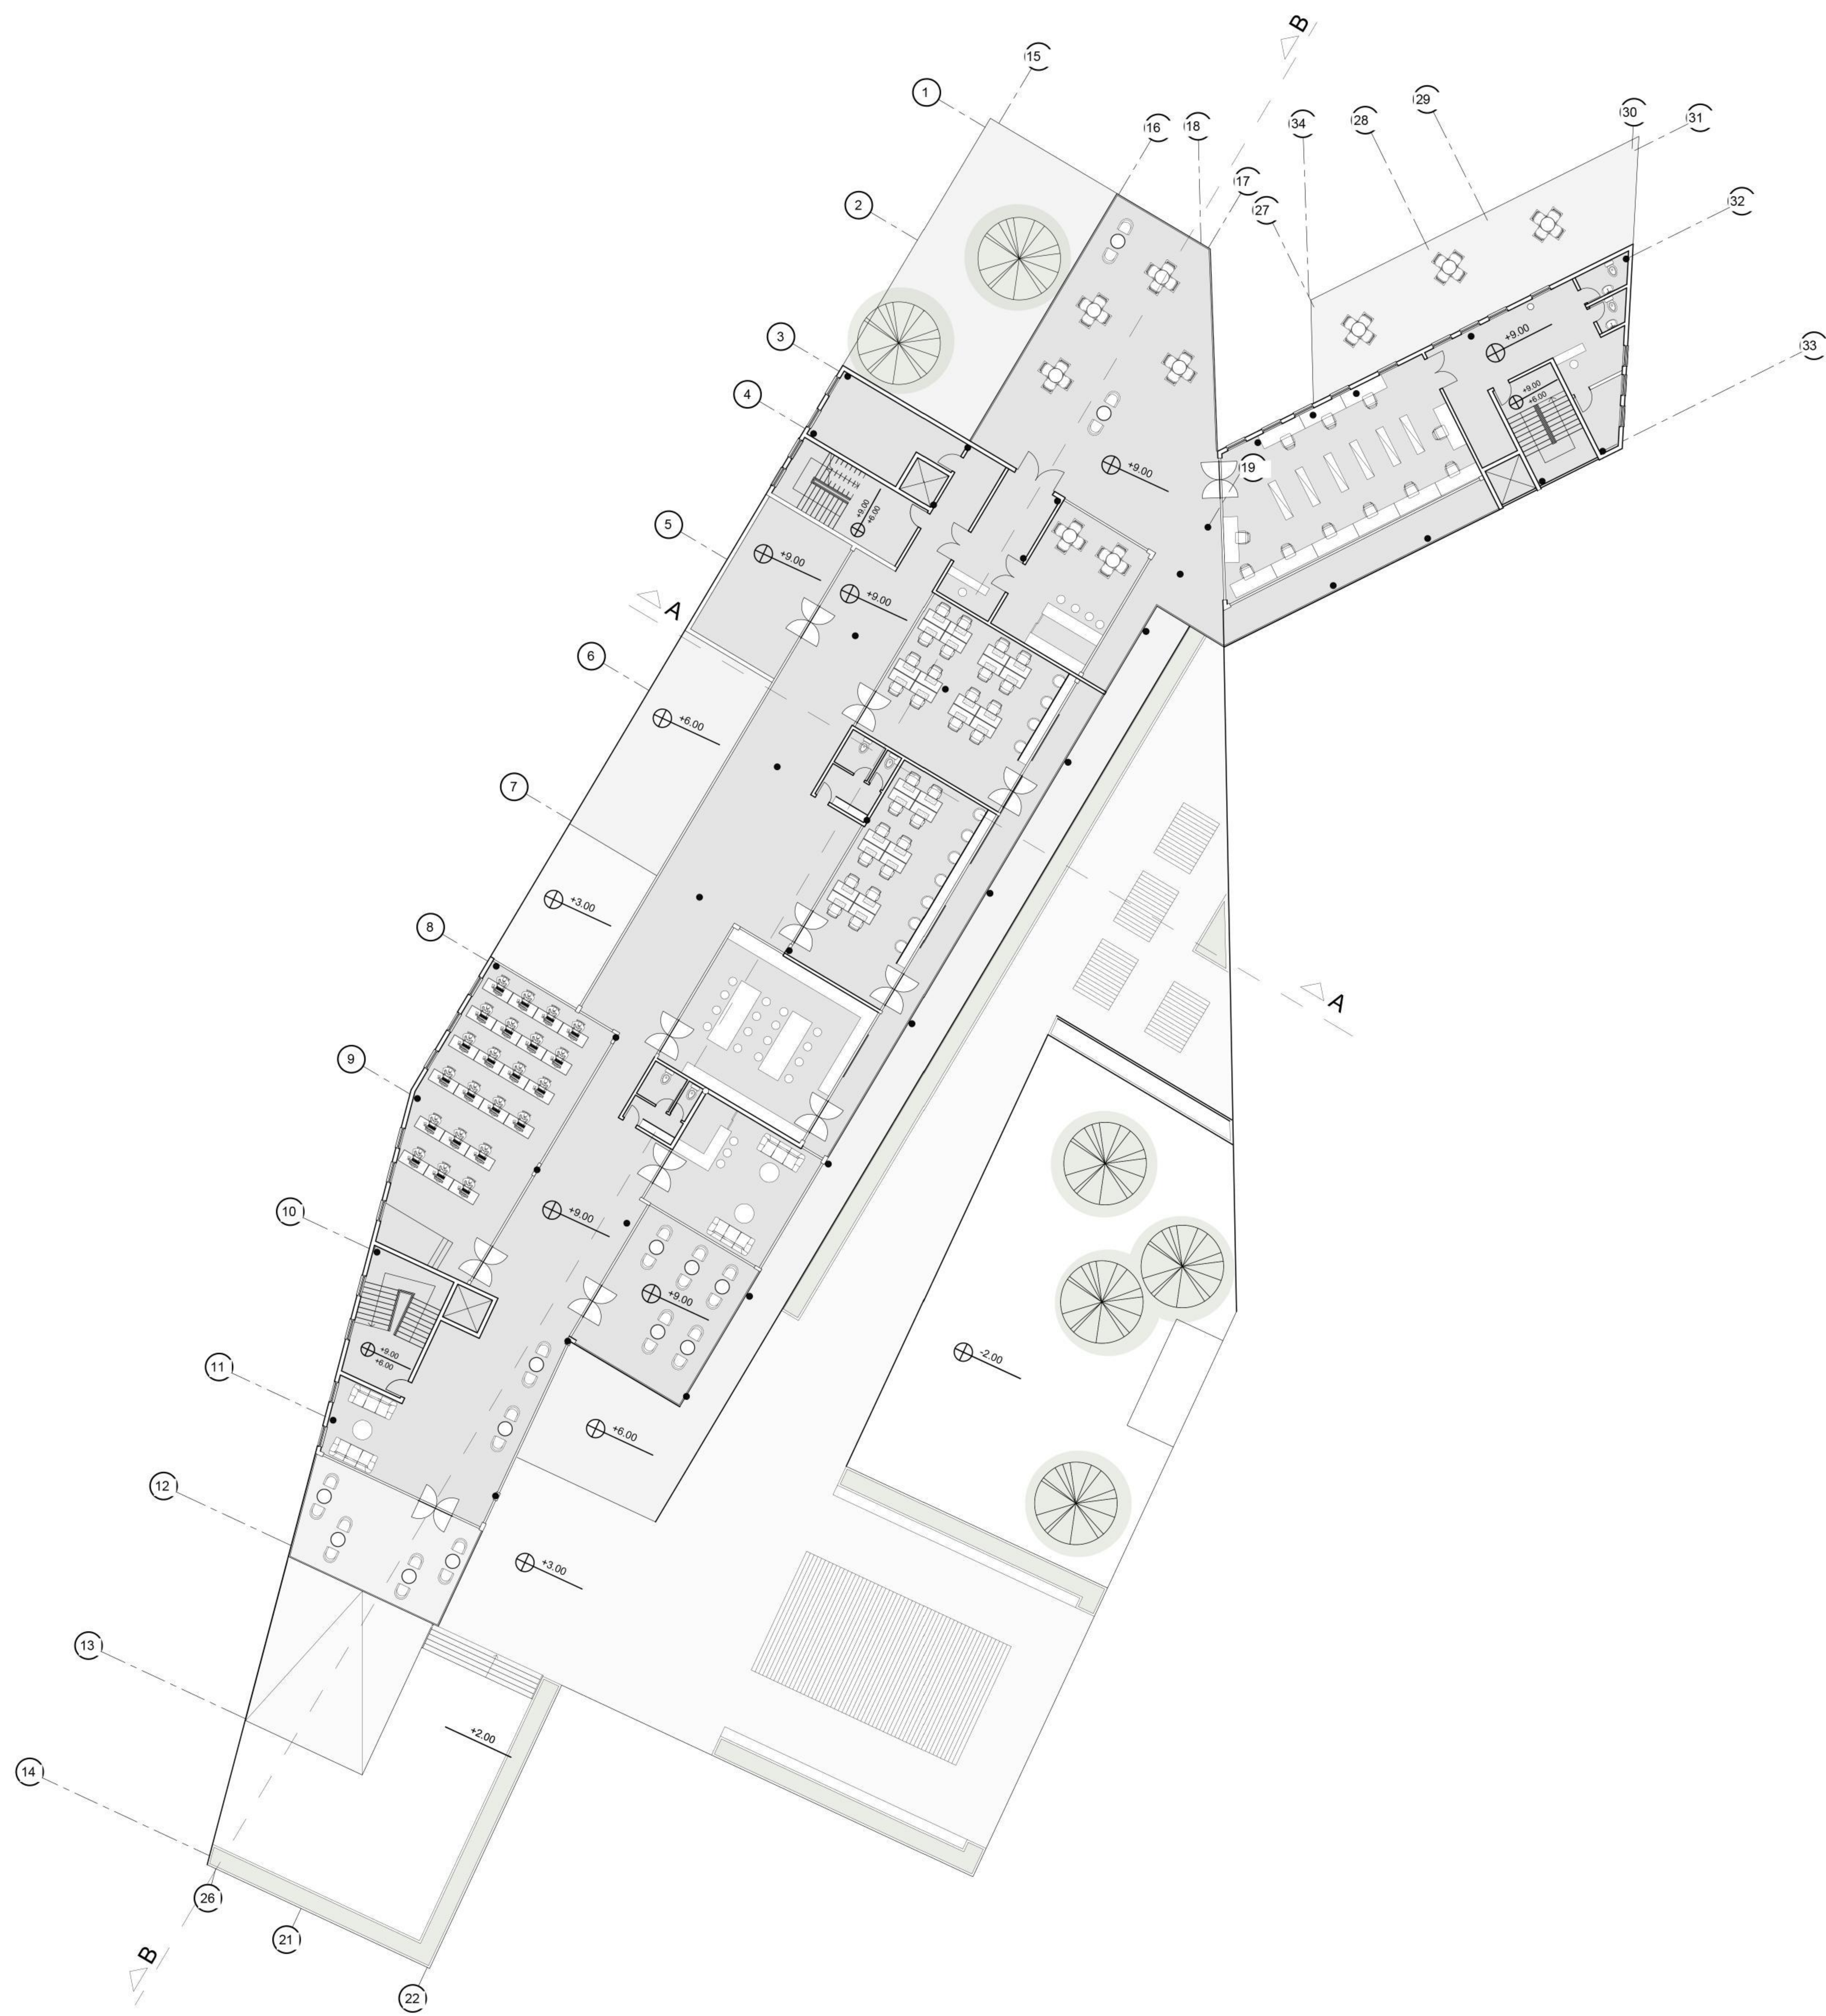



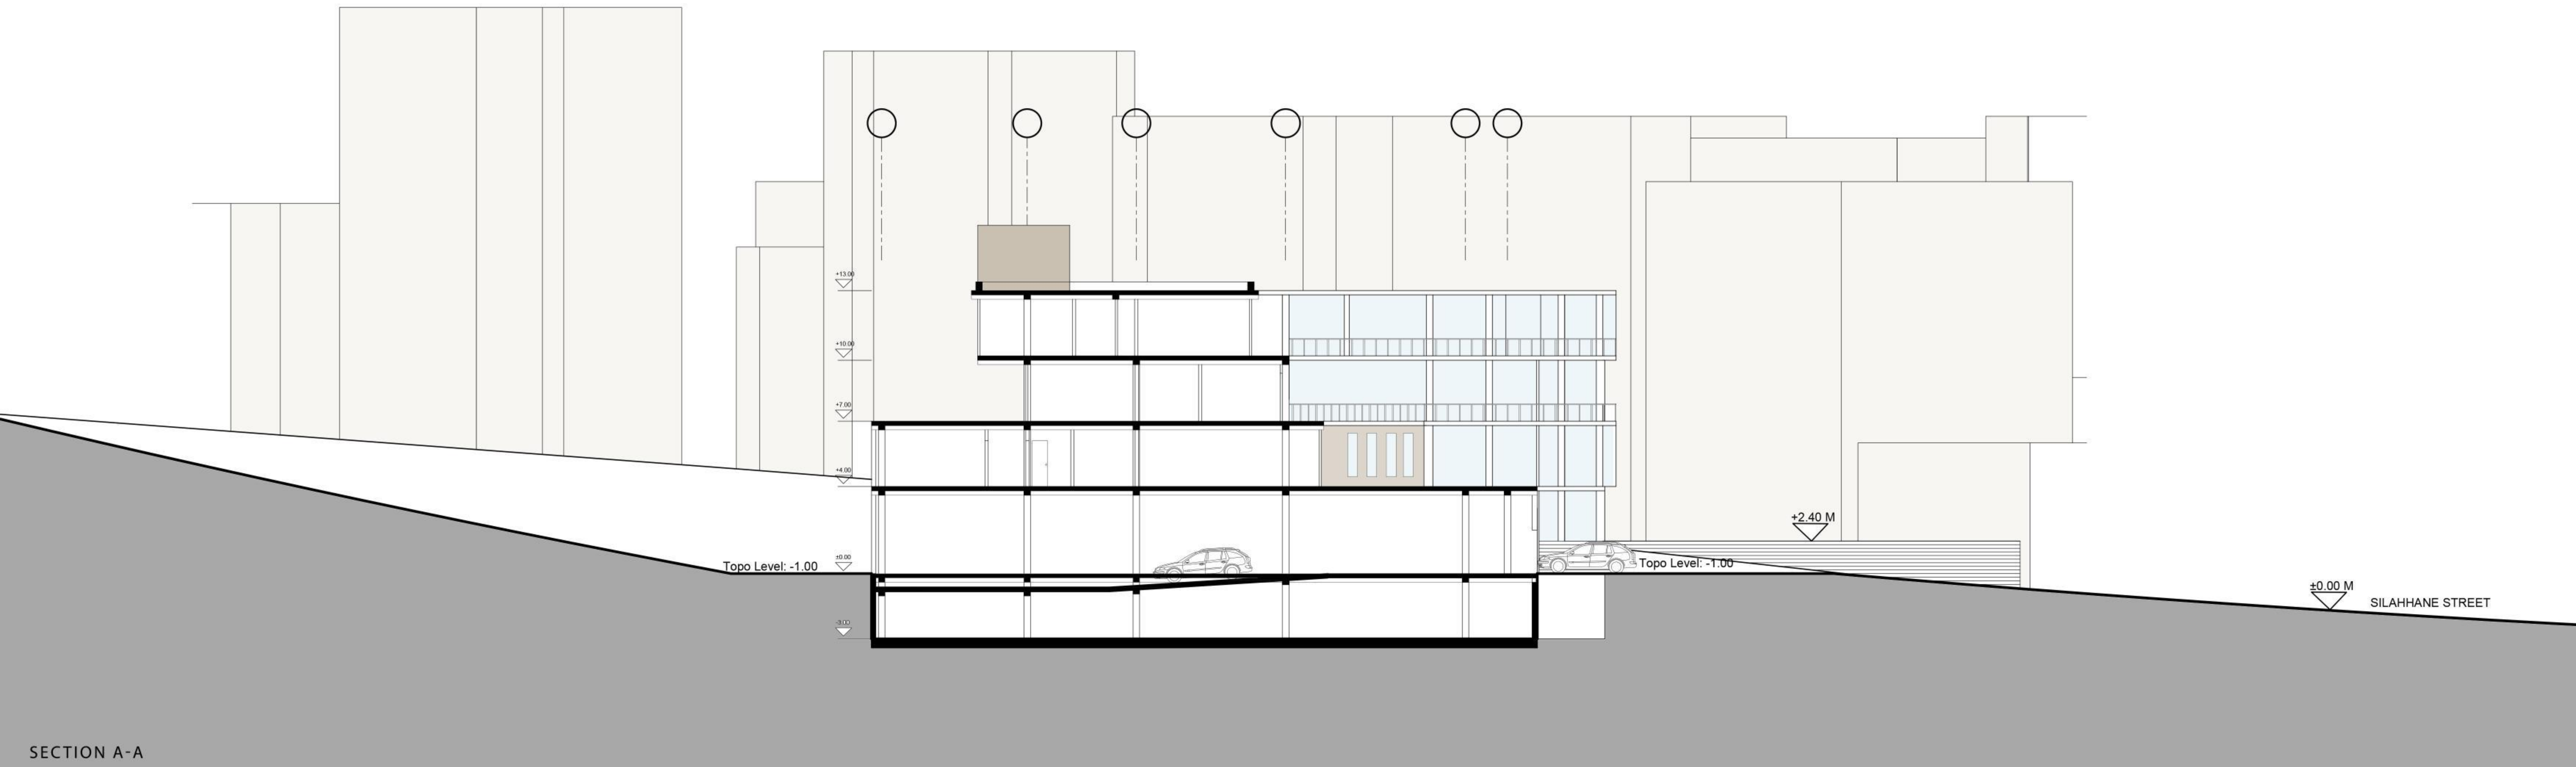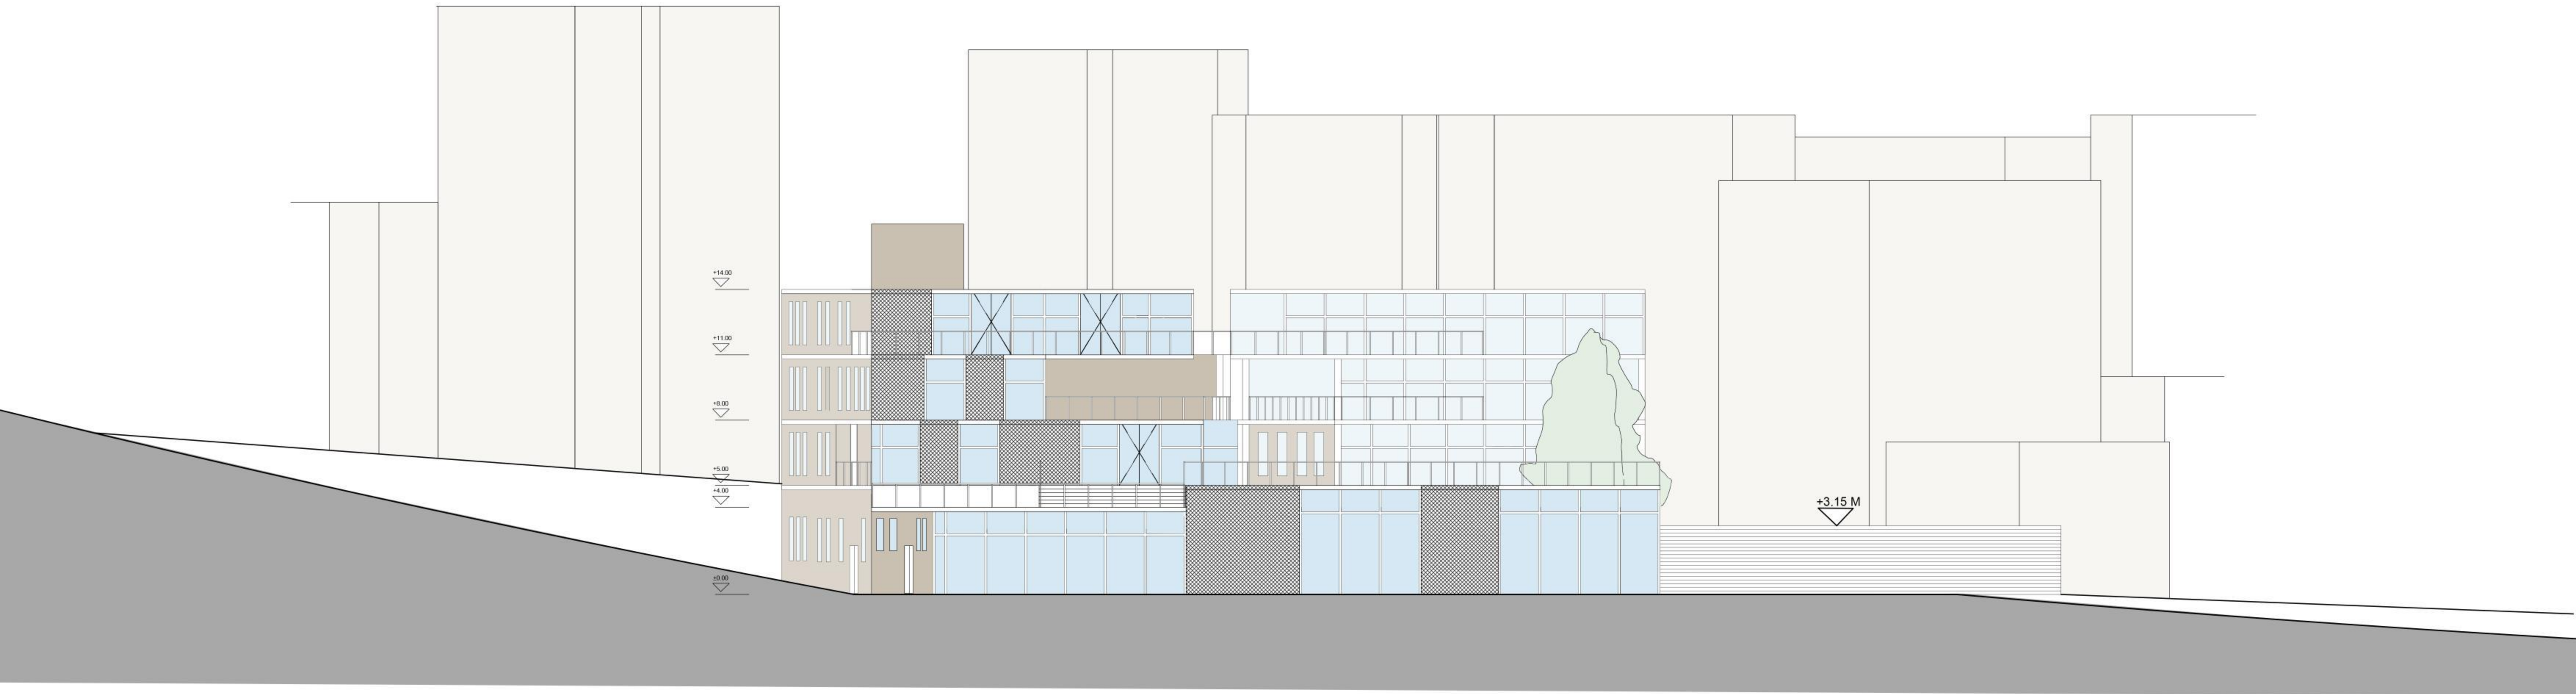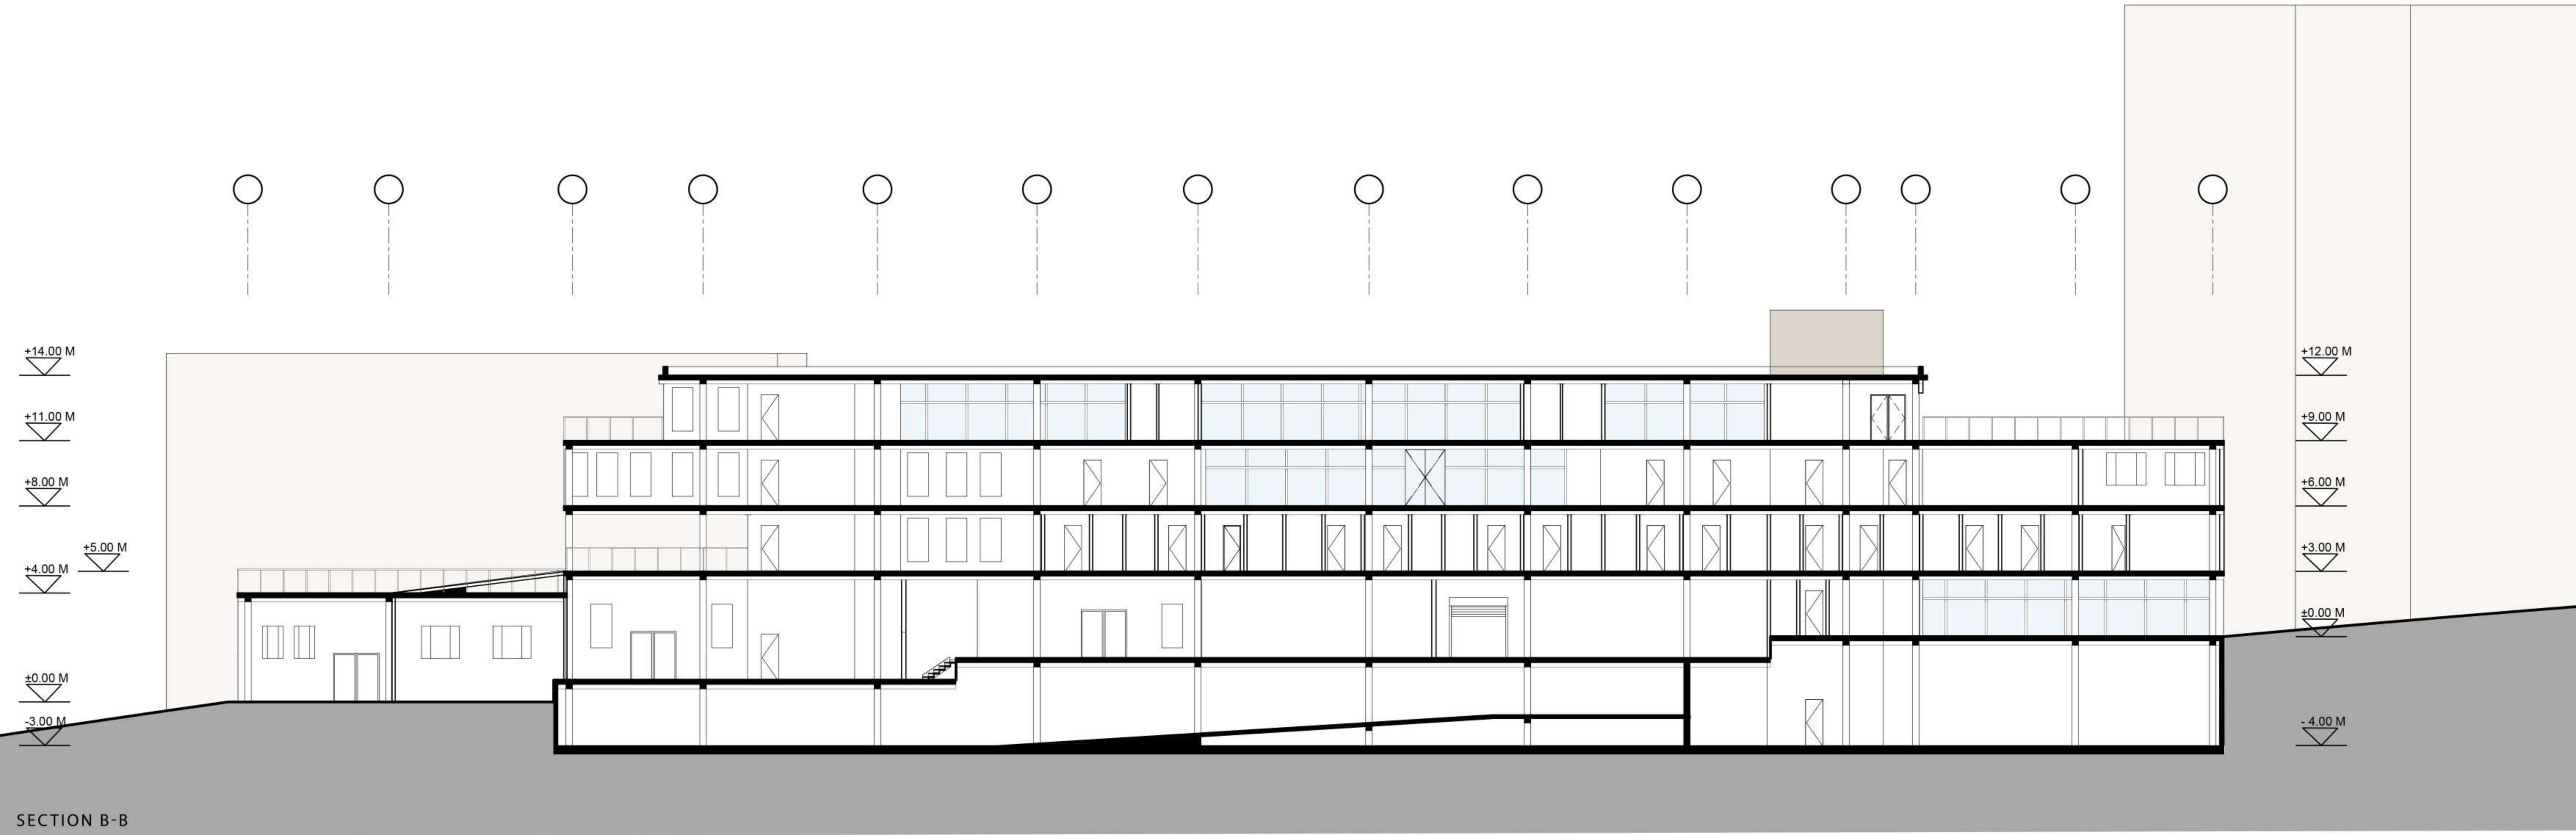

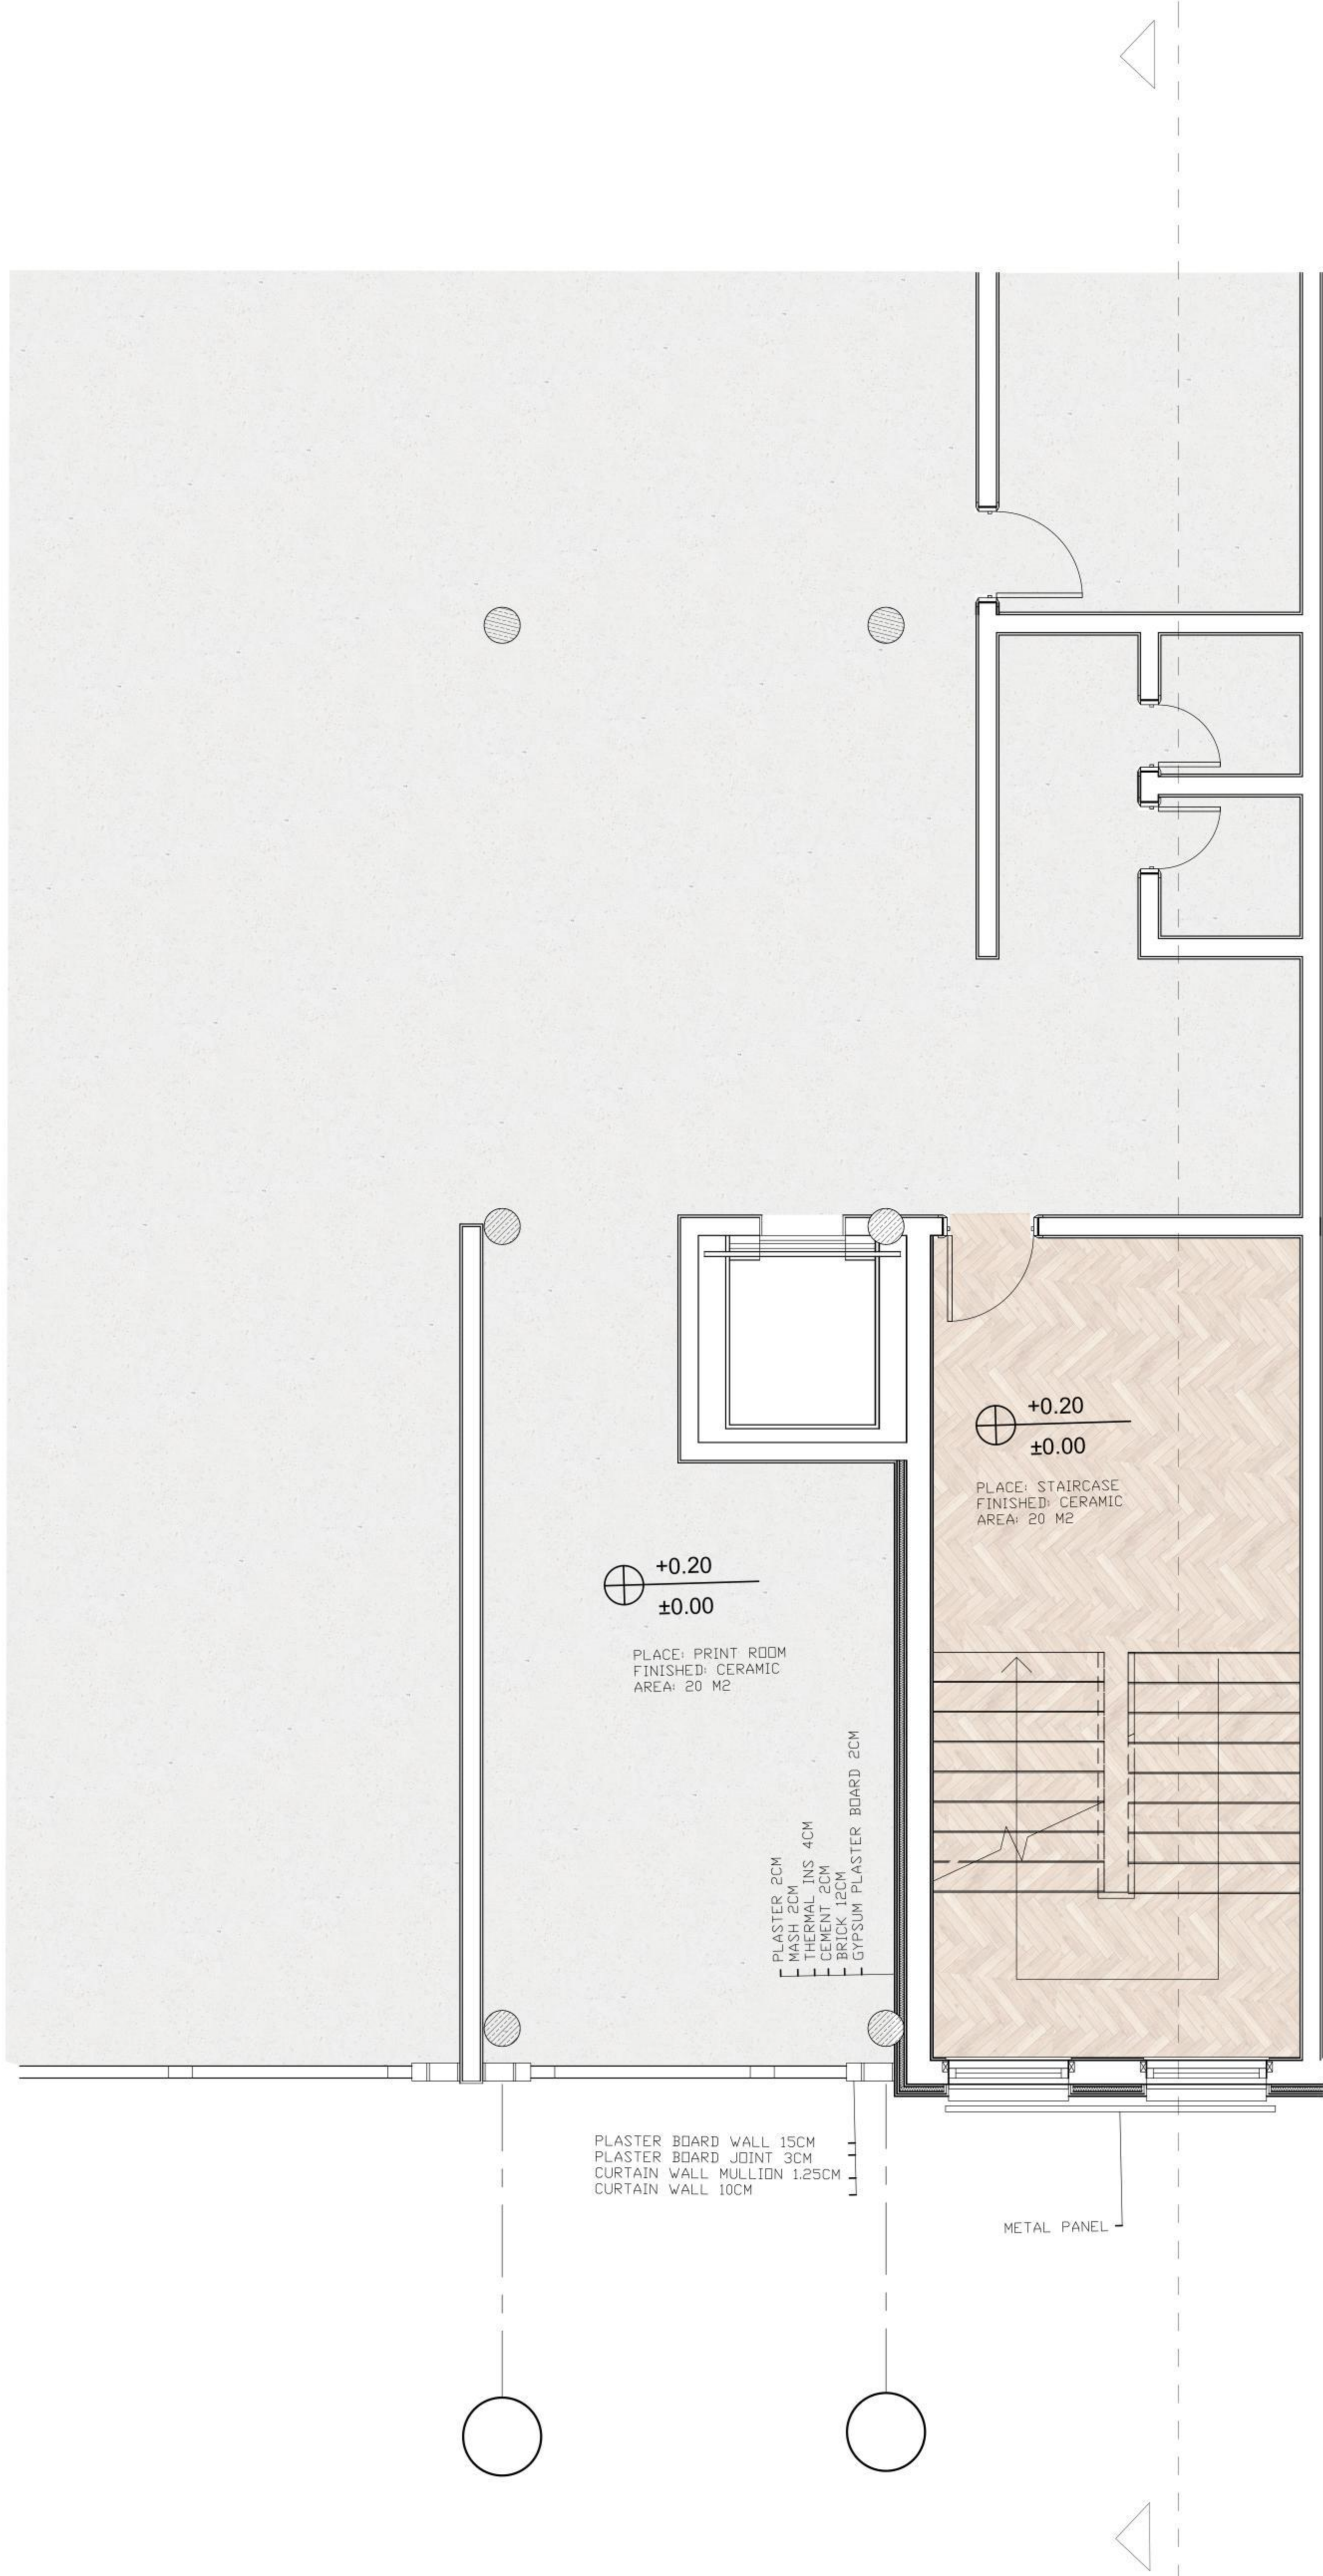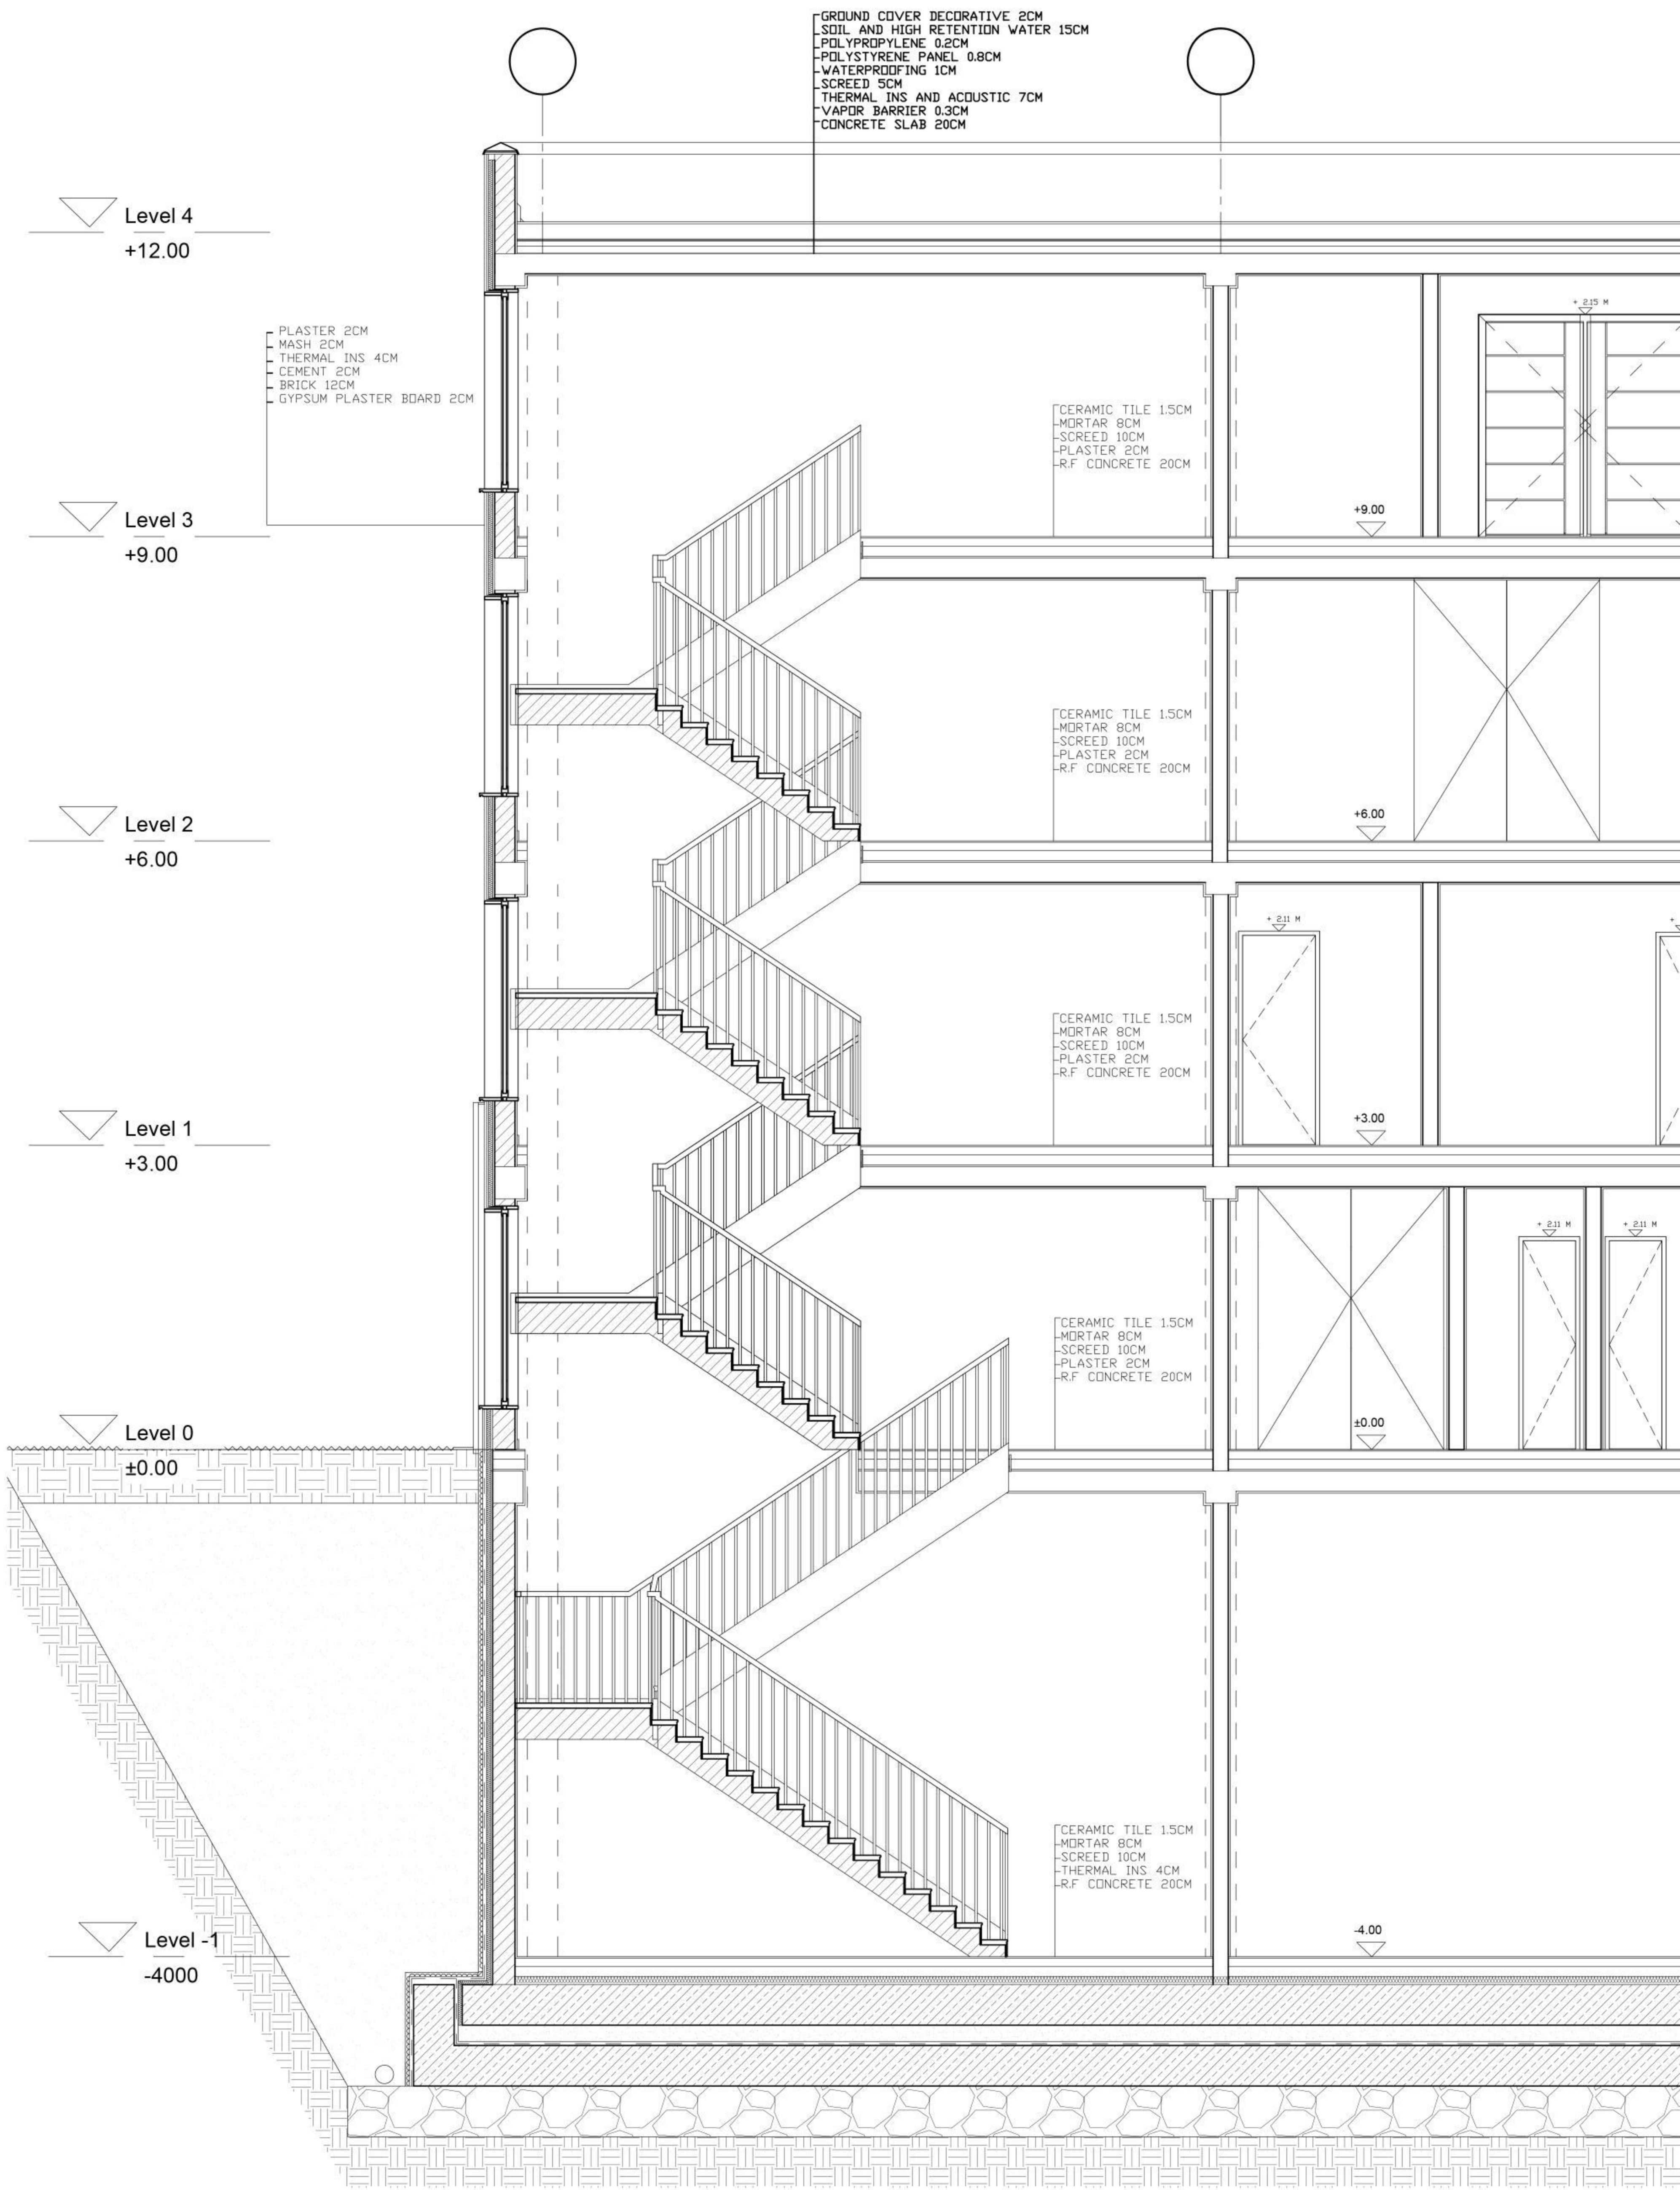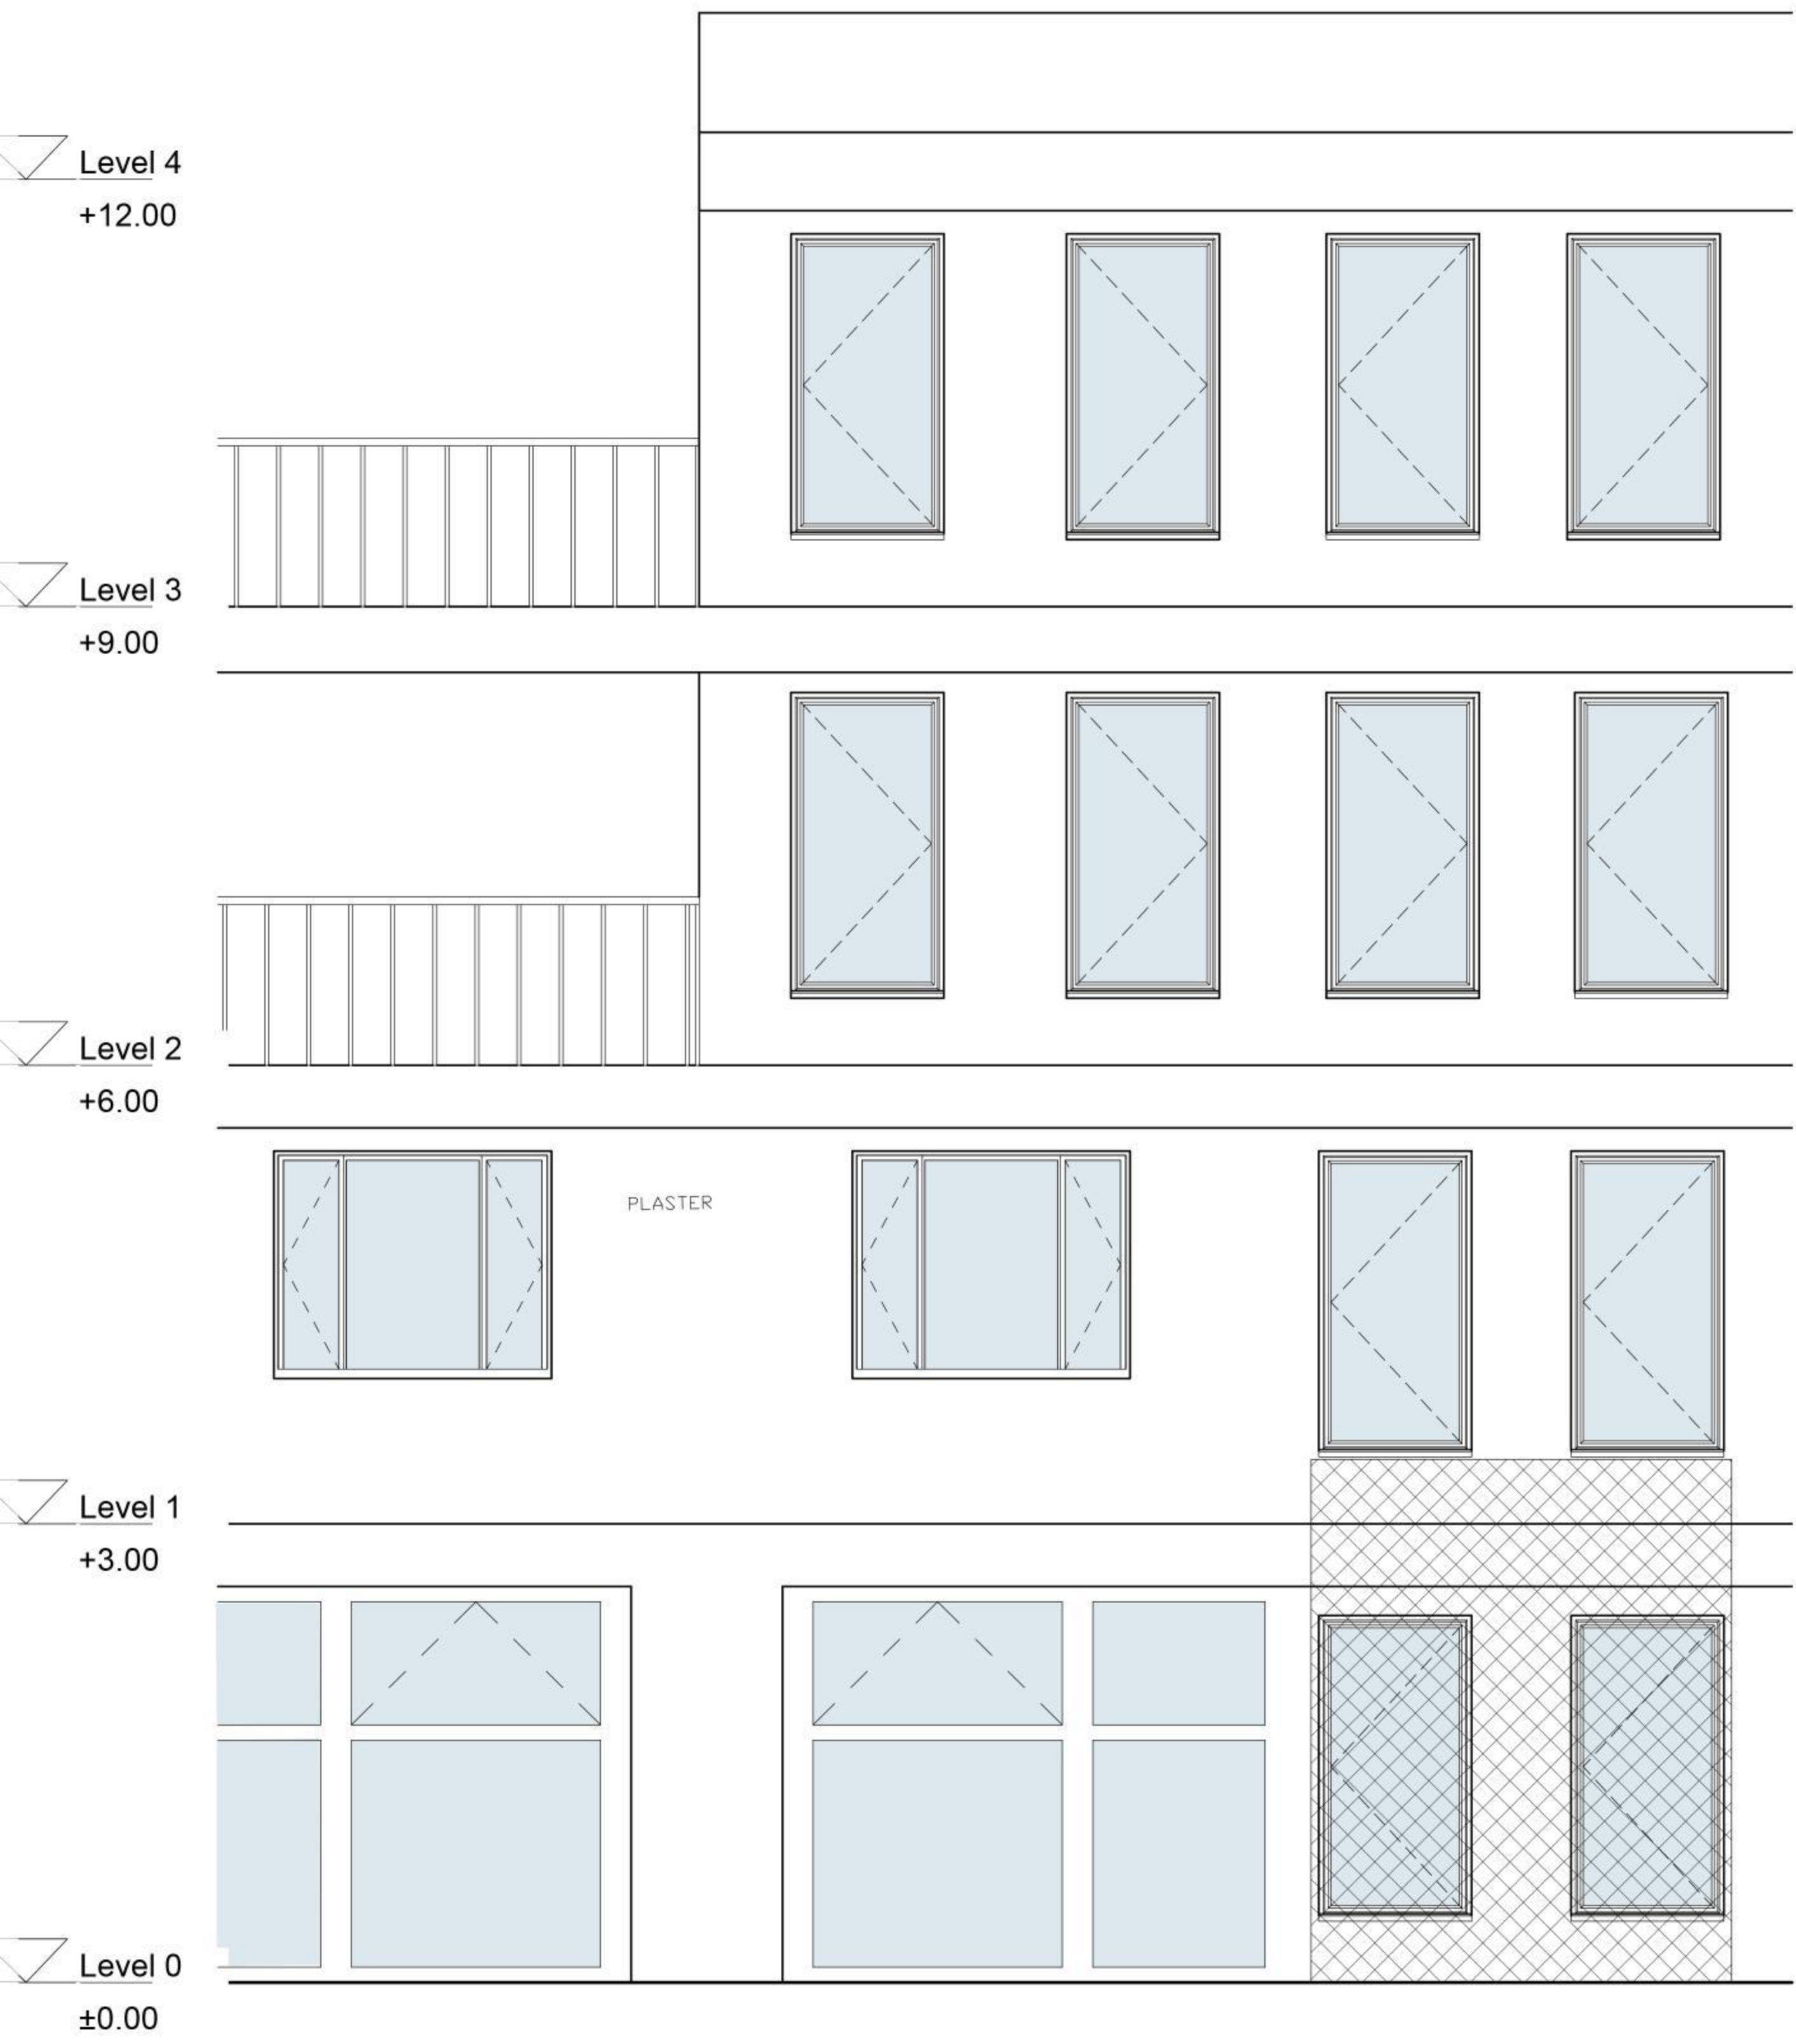

“METAL MESH WINDOW SCREEN”

- IT HAS RAILING
- IT IS NOT FIXED
- IT CAN MOVE BY HUMAN CONTROLLING
- IT PROVIDES SHADE, ALLOW VENTILATION, ENHANCE SECURITY, AND CAN BE DESIGNED IN VARIOUS PATTERNS FOR AESTHETIC APPEAL WHILE PROMOTING ENERGY EFFICIENCY IN BUILDINGS.

